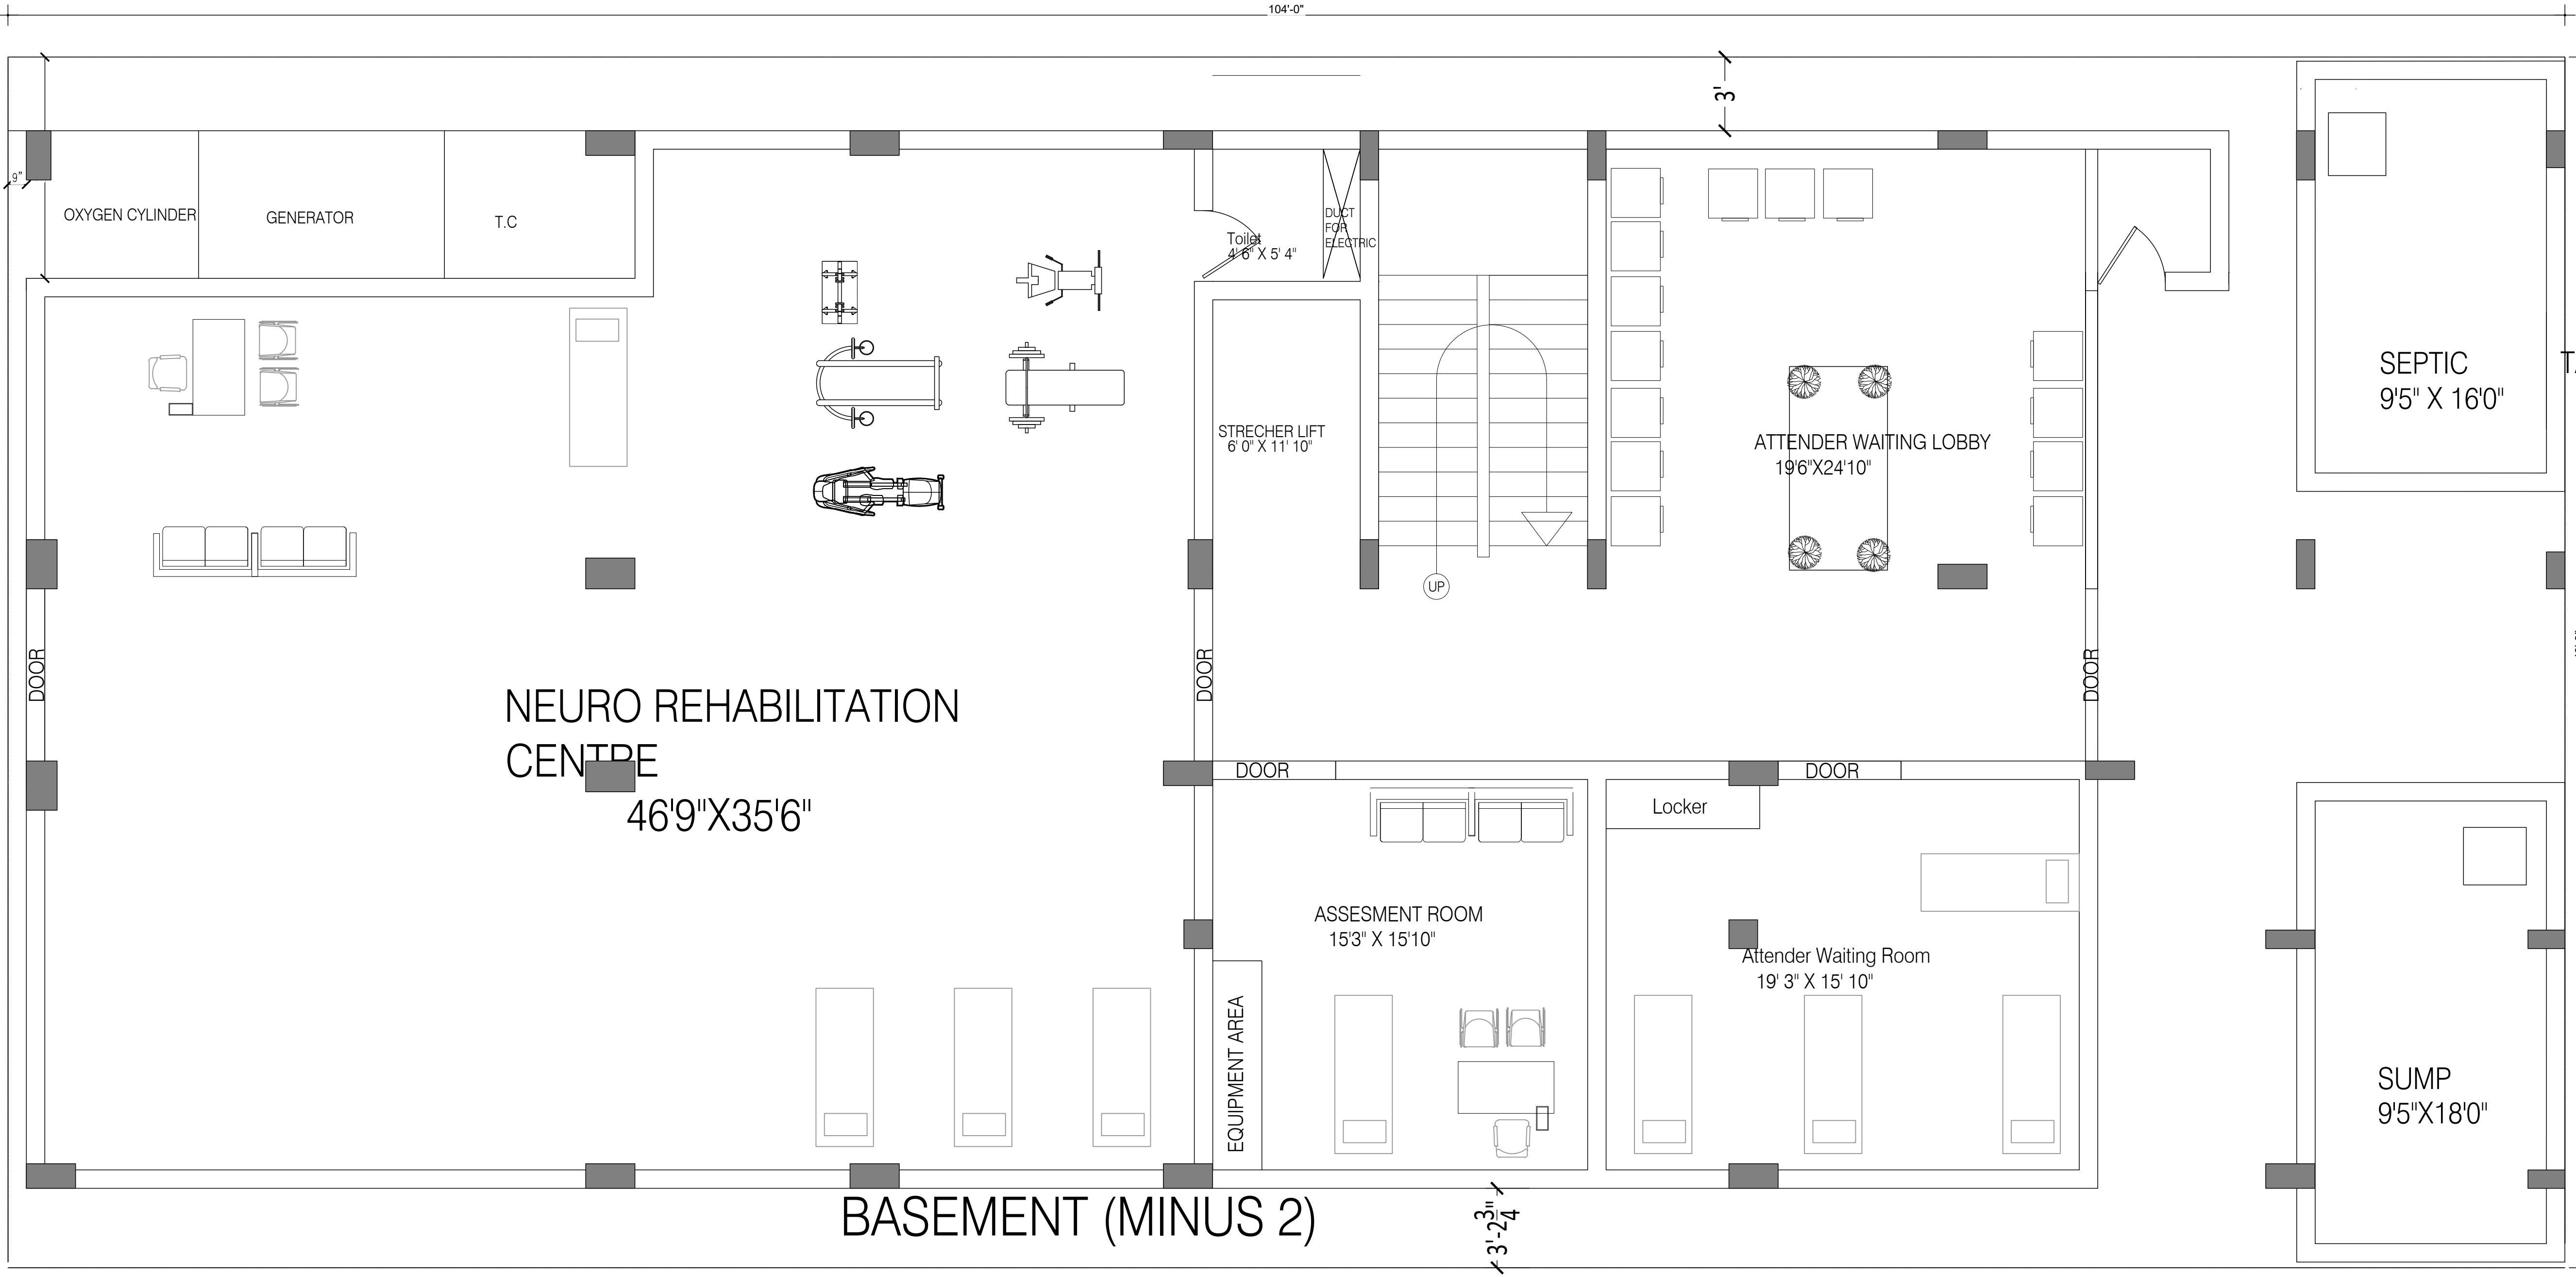




NOTES:-

CLEAR FLOOR HEIGHT :-

FLOOR HEIGHT :- 10'-6"

STAIRS DETAILS :-

EX. STAIRCASE TREAD = 10"

IN. STAIRCASE TREAD = 12"

EX RISER = 6.28"

IN RISER = 5.07"

EX. NUMBER OF STAIRS =21

IN. NUMBER OF STAIRS =26

WALL SIZE :-

OUTER WALLS = 9"

PARTITION WALLS = 5"

LEVEL :-

PARKING LVL. = -18'-6"

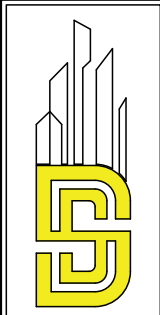
PLINTH LVL. = +3'-0"

TANK FOR ,



VIRAJ
CONSTRUCTIONS

DESIGNED BY ,




DREAMSTEP
DESIGN AND
CONSTRUCTIONS


DRAWN	VIDHYA
CHECKED	PRAJWAL
REV.NO.	

PROJECT: RESIDENTIAL

CLIENT NAME : Dr . RAKESH . A V

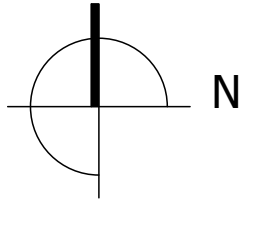TITLE: GROUND FLOOR

DIRECTION :

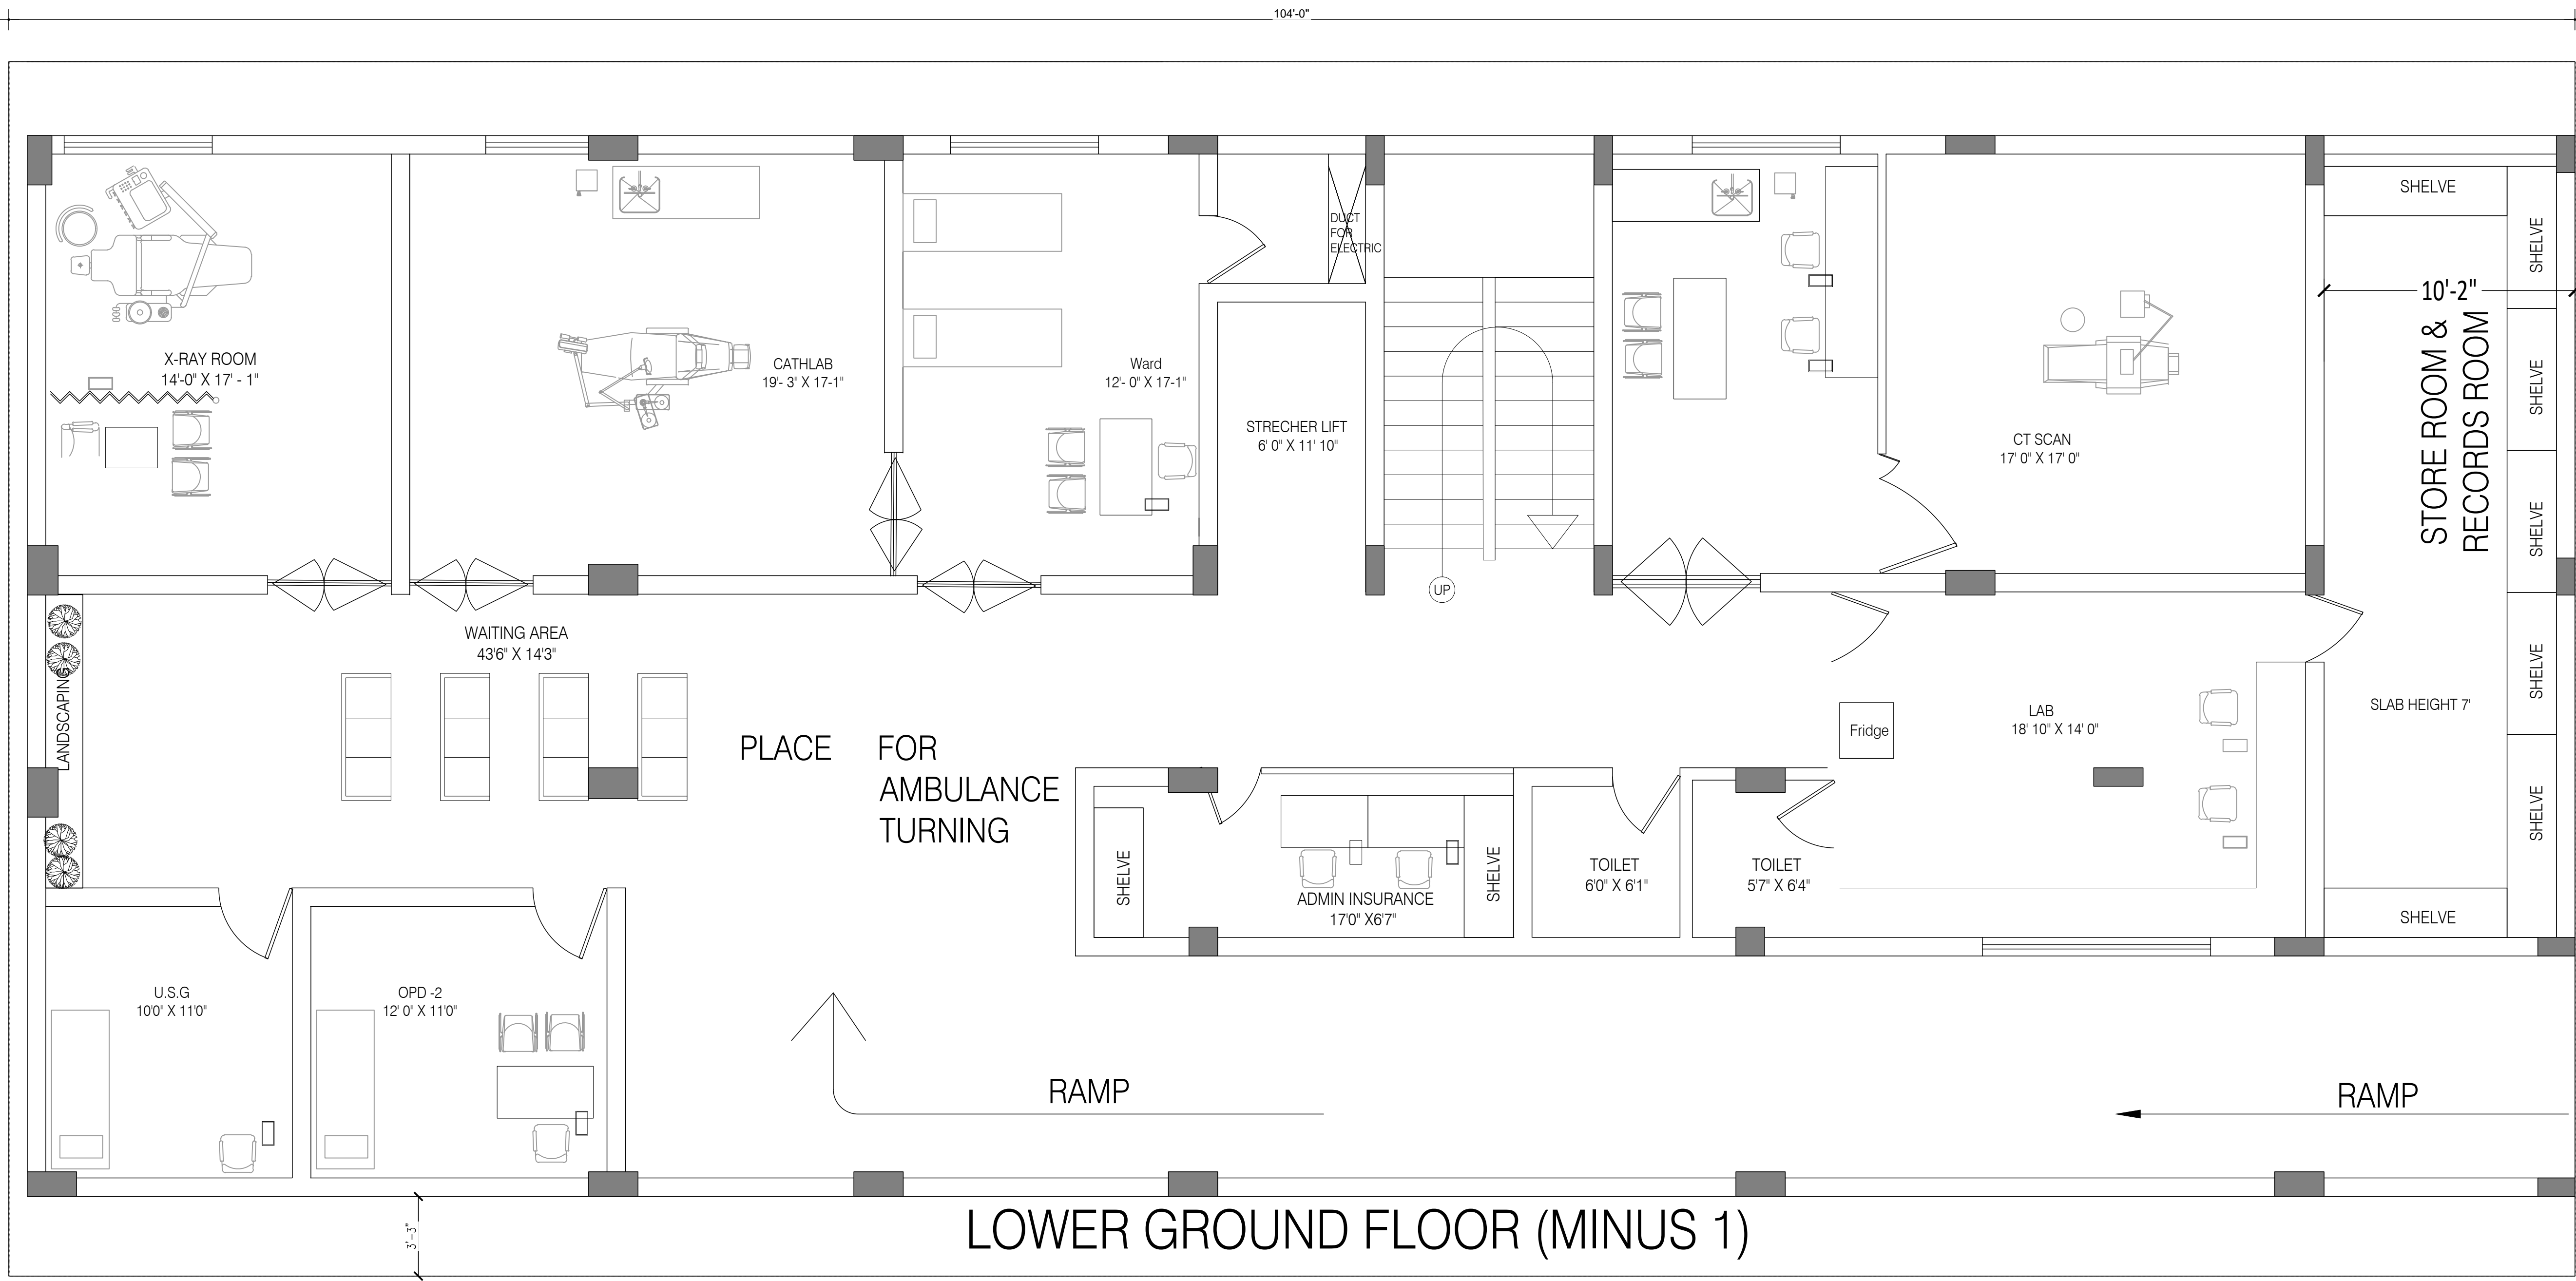


NOTES:-

CLEAR FLOOR HEIGHT :-

FLOOR HEIGHT :- 10'-6"

STAIRS DETAILS :-

EX. STAIRCASE TREAD = 10"

IN. STAIRCASE TREAD = 12"

EX RISER = 6.28"

IN RISER = 5.07"

EX. NUMBER OF STAIRS =21

IN. NUMBER OF STAIRS =26

WALL SIZE :-

OUTER WALLS = 9"

PARTITION WALLS = 5"

LEVEL :-

PARKING LVL. = -18'-6"

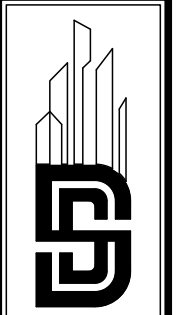
PLINTH LVL. = +3'-0"

FOR ,



VIRAJ
CONSTRUCTIONS

DESIGNED BY ,



DREAMSTEP
DESIGN AND
CONSTRUCTIONS


DRAWN	PRAJWAL
CHECKED	PRAJWAL
REV.NO.	


PROJECT: RESIDENTIAL

CLIENT NAME : Dr . RAKESH . A V

TITLE: FIRST FLOOR

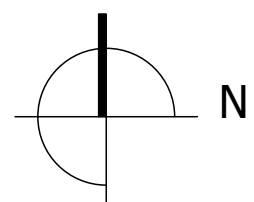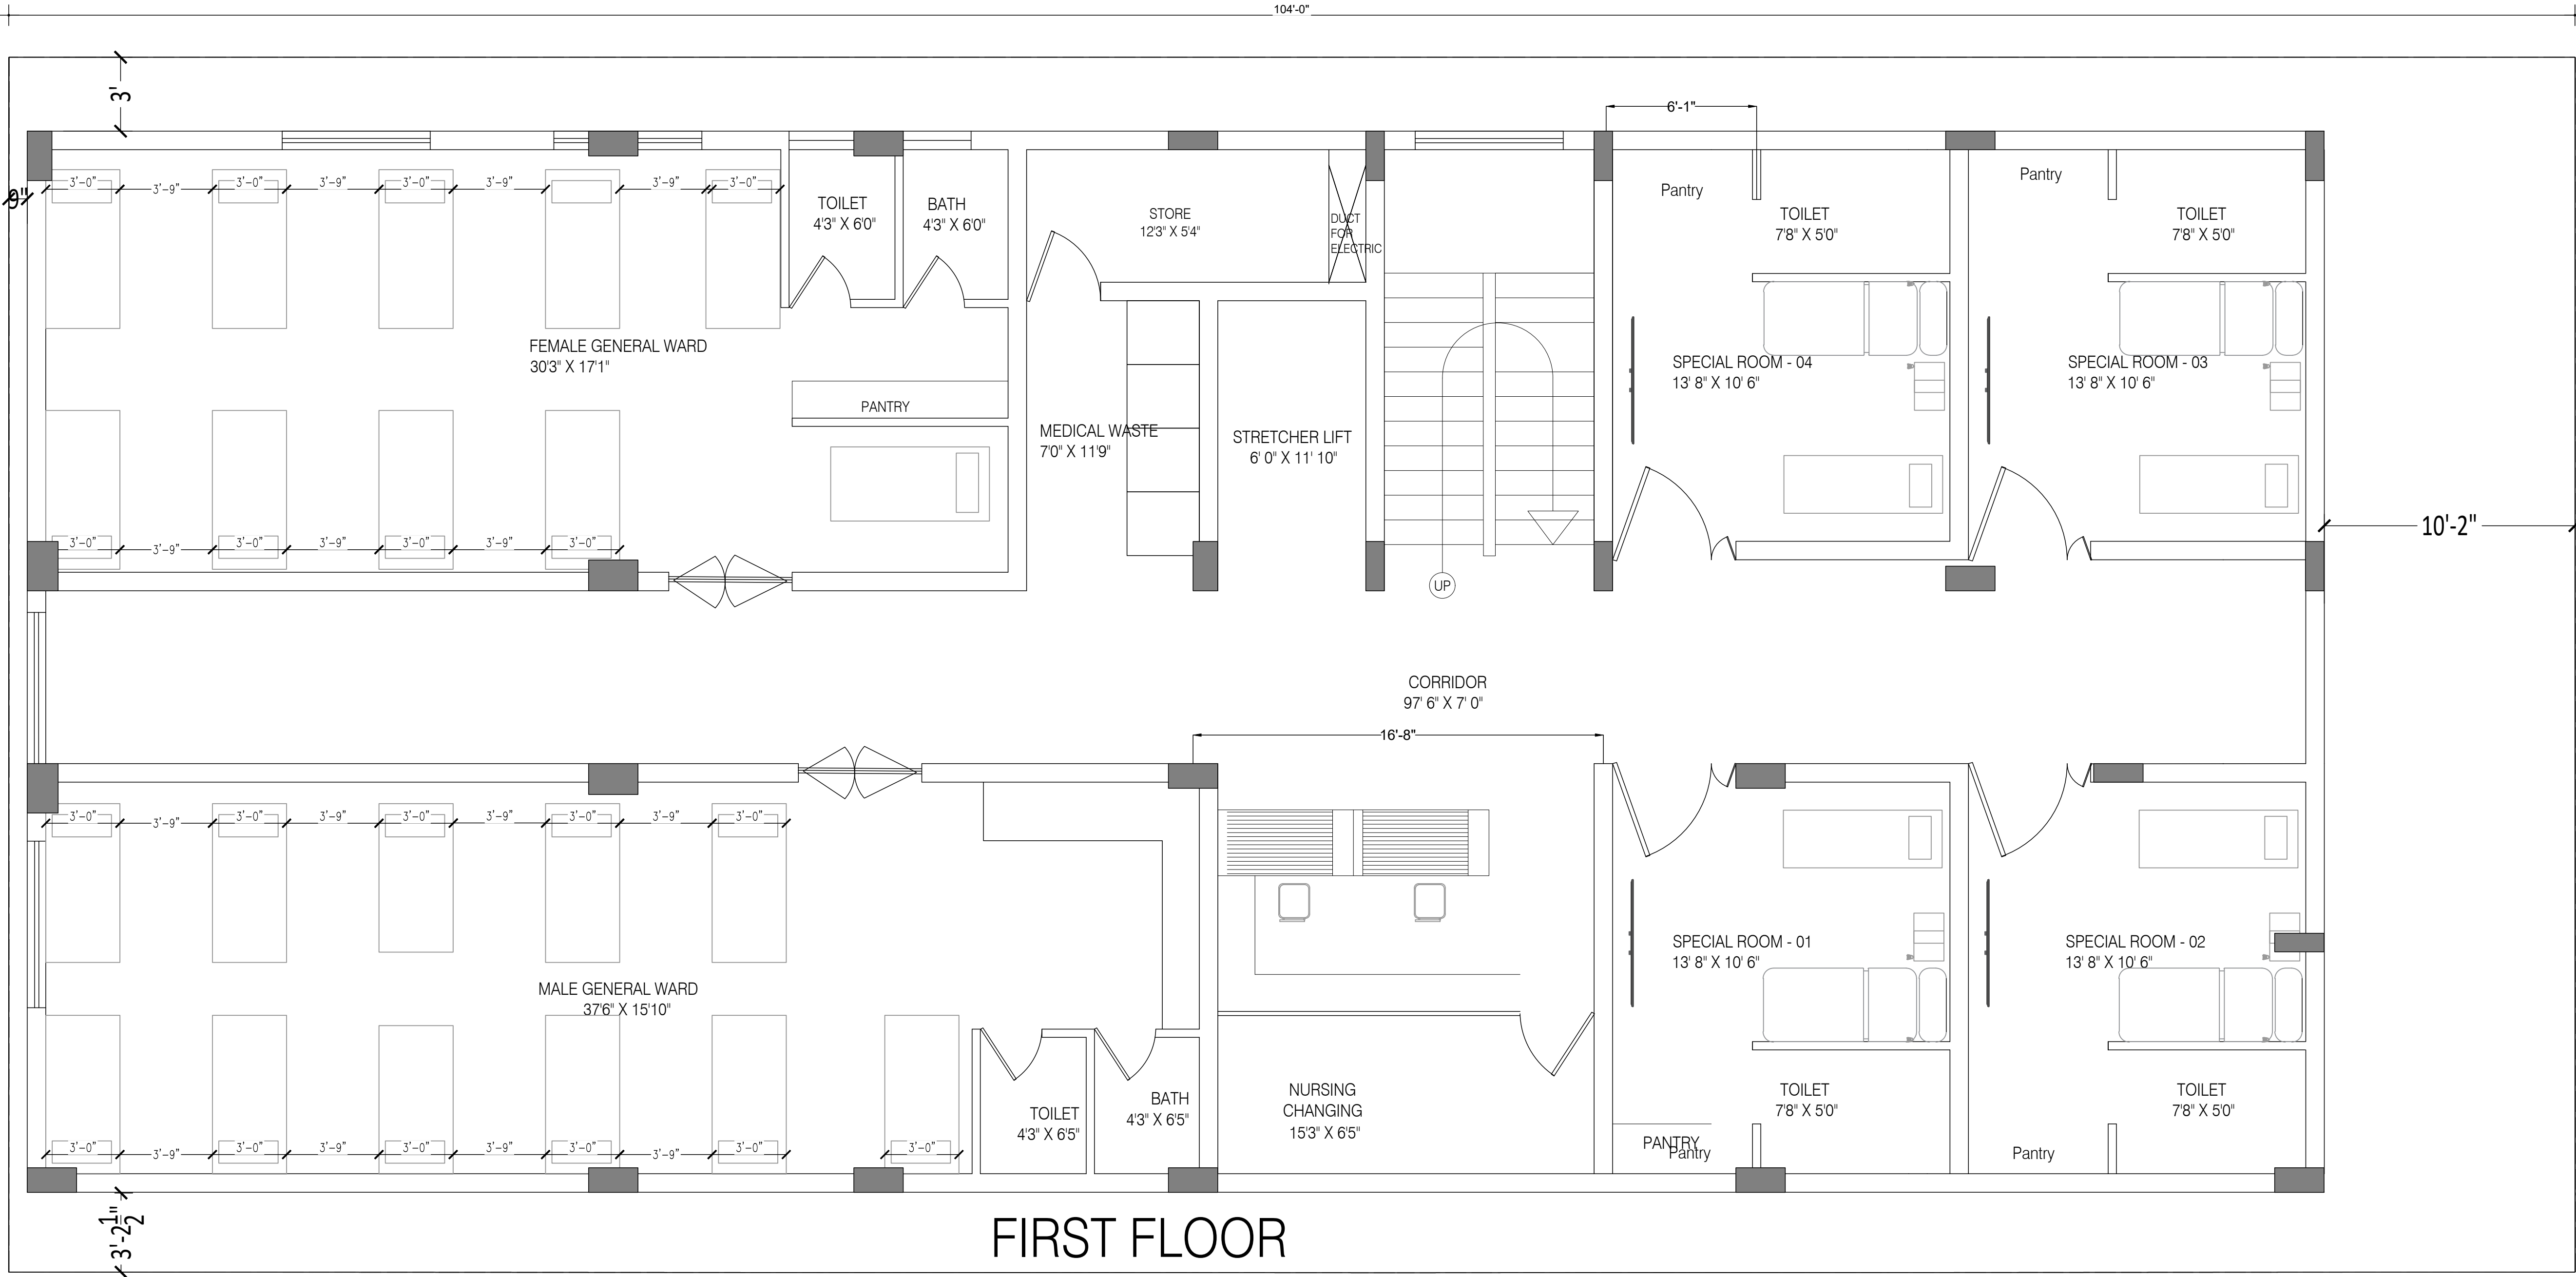DIRECTION :





NOTES:-

CLEAR FLOOR HEIGHT :-

FLOOR HEIGHT :- 10'-6"

STAIRS DETAILS :-

EX. STAIRCASE TREAD = 10"

IN. STAIRCASE TREAD = 12"

EX RISER = 6.28"

IN RISER = 5.07"

EX. NUMBER OF STAIRS =21

IN. NUMBER OF STAIRS =26

WALL SIZE :-

OUTER WALLS = 9"

PARTITION WALLS = 5"

LEVEL :-

PARKING LVL. = -18'-6"

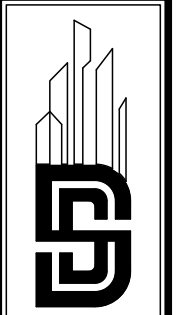
PLINTH LVL. = +3'-0"

FOR ,



VIRAJ
CONSTRUCTIONS

DESIGNED BY ,



DREAMSTEP
DESIGN AND
CONSTRUCTIONS


DRAWN	PRAJWAL
CHECKED	PRAJWAL
REV.NO.	


PROJECT: RESIDENTIAL

CLIENT NAME : Dr . RAKESH . A V

TITLE: FIRST FLOOR

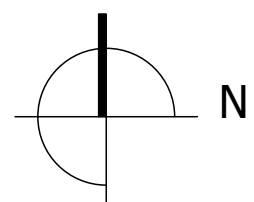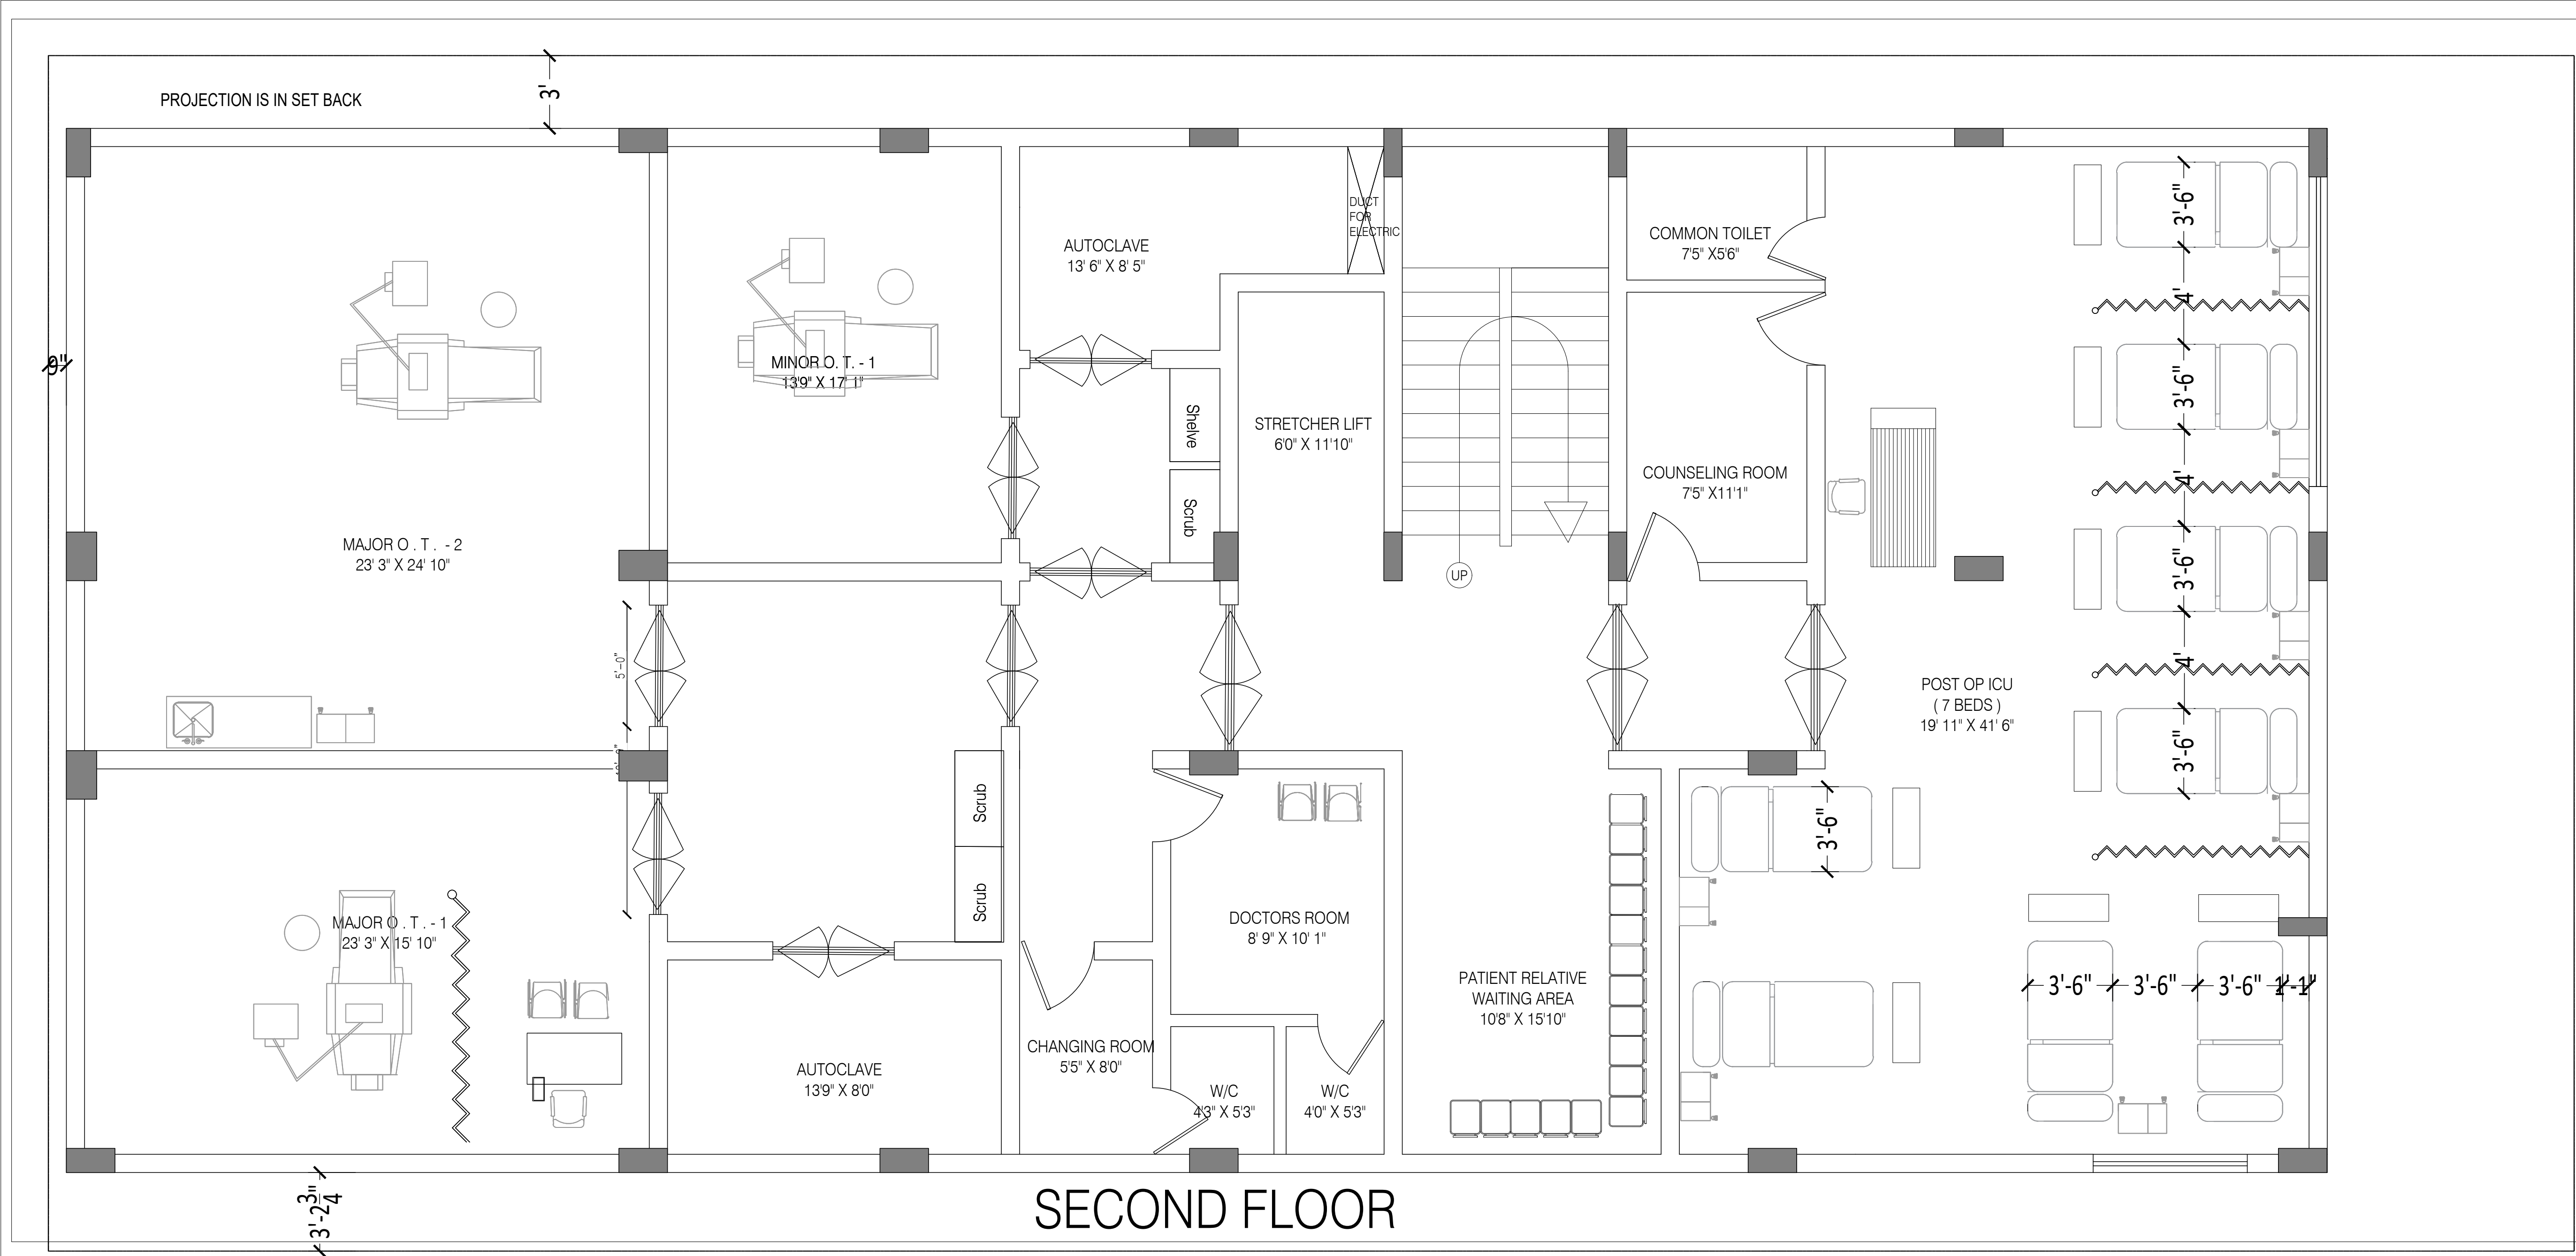DIRECTION :





NOTES:-

CLEAR FLOOR HEIGHT :-

FLOOR HEIGHT :- 10'-6"

STAIRS DETAILS :-

EX. STAIRCASE TREAD = 10"

IN. STAIRCASE TREAD = 12"

EX RISER = 6.28"

IN RISER = 5.07"

EX. NUMBER OF STAIRS =21

IN. NUMBER OF STAIRS =26

WALL SIZE :-

OUTER WALLS = 9"

PARTITION WALLS = 5"

LEVEL :-

PARKING LVL. = -18'-6"

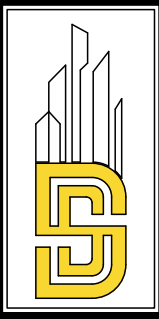
PLINTH LVL. = +3'-0"

FOR ,



VIRAJ
CONSTRUCTIONS

DESIGNED BY ,



DREAMSTEP
DESIGN AND
CONSTRUCTIONS


DRAWN	PRAJWAL
CHECKED	PRAJWAL
REV.NO.	


PROJECT: RESIDENTIAL

CLIENT NAME : Dr . RAKESH . A V

TITLE: SECOND FLOOR

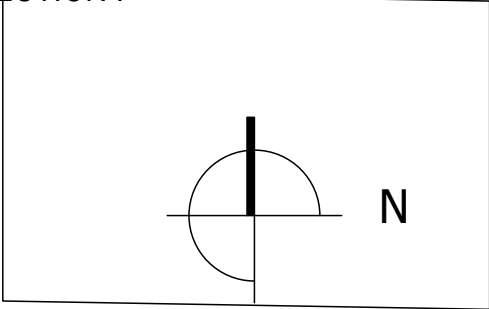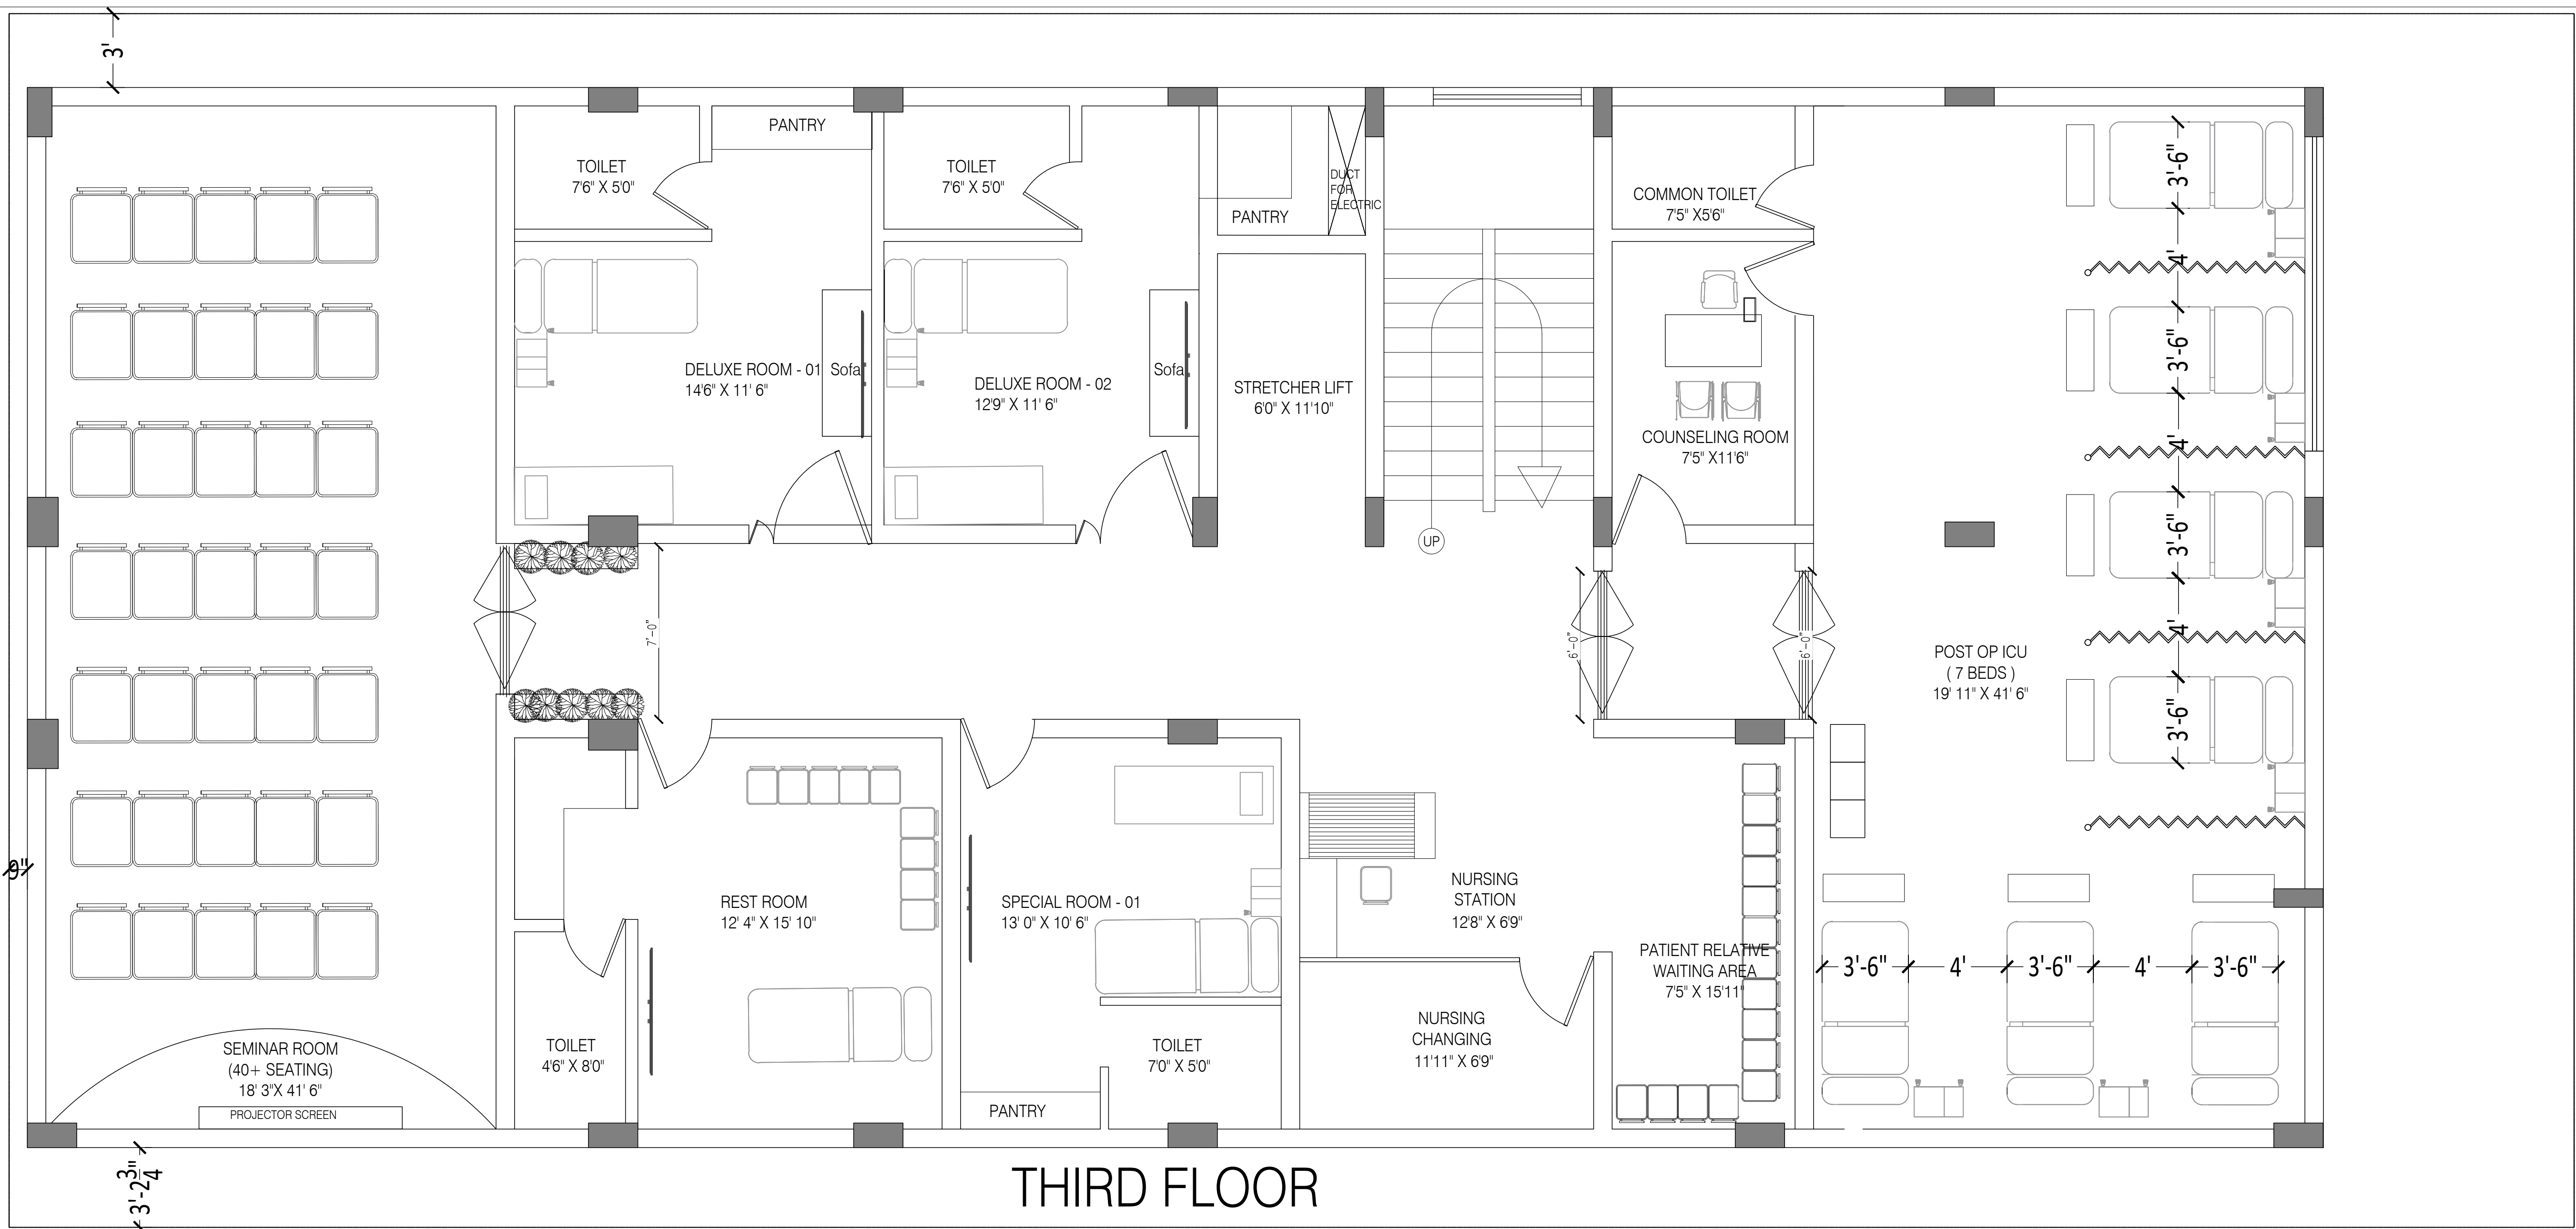DIRECTION :-





NOTES:-

CLEAR FLOOR HEIGHT :-

FLOOR HEIGHT :- 10'-6"

STAIRS DETAILS :-

EX. STAIRCASE TREAD = 10"

IN. STAIRCASE TREAD = 12"

EX RISER = 6.28"

IN RISER = 5.07"

EX. NUMBER OF STAIRS =21

IN. NUMBER OF STAIRS =26

WALL SIZE :-

OUTER WALLS = 9"

PARTITION WALLS = 5"

LEVEL :-

PARKING LVL. = -18'-6"

PLINTH LVL. = +3'-0"

FOR ,



VIRAJ

CONSTRUCTIONS

DESIGNED BY ,



DREAMSTEP

DESIGN AND

CONSTRUCTIONS


DRAWN	VIDHYA
CHECKED	PRAJWAL
REV.NO.	


PROJECT: RESIDENTIAL

CLIENT NAME : Dr . RAKESH . A V

TITLE: THIRD FLOOR

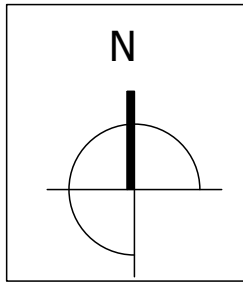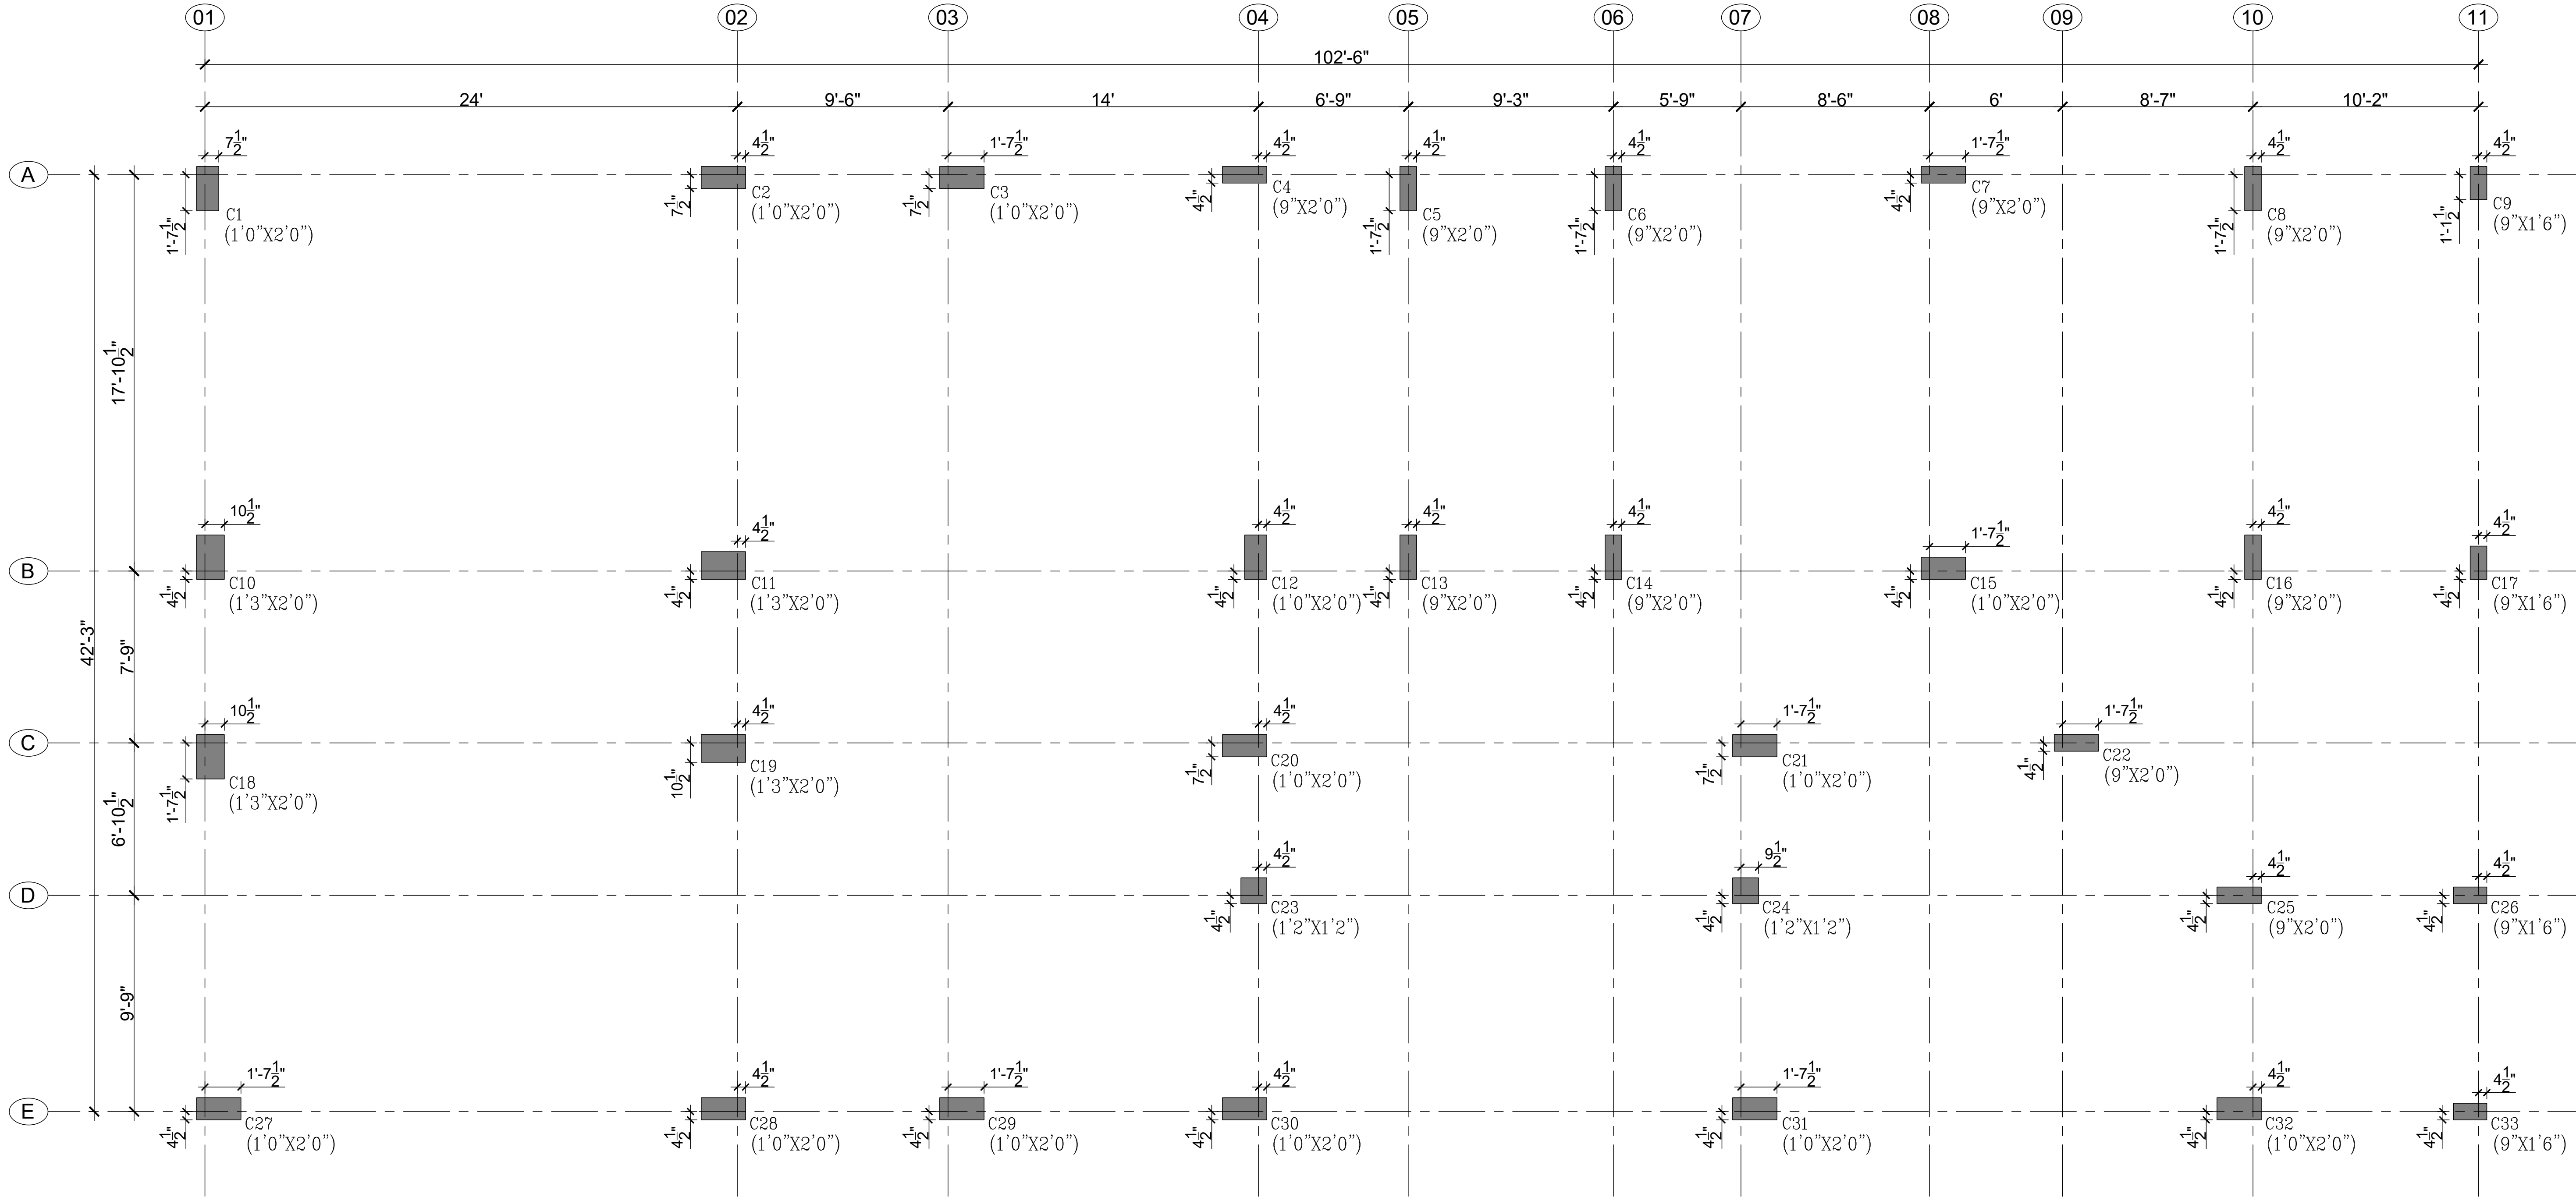DIRECTION :






COLUMN LAYOUT

- GENERAL NOTES:-**
- THIS DRAWING TO BE READ IN CONJUNCTION WITH THE RELEVANT ARCHITECTURAL AND SERVICES DRAWINGS.
 - BUILDING DESIGNED FOR B1+B2+G+3 FLOORS.
 - GRADE OF CONCRETE FOR ALL RCC MEMBERS IN THE BUILDING IS M25.
 - AT THE LOCATION WHERE FOOTING IS RESTING SBC IS 20.00T/SQ-M @5'0" MIN. FROM NGL. SBC SHALL BE RACTIFIED BEFORE LAYING THE PCC FROM CONSULTING PROFESSIONAL.
 - FOR SETTING OUT OF THE BUILDING REFER ARCHITECTURAL DRAWING.
 - COMBINED FOOTING CONCRETING TO BE DONE CONTINUOUSLY IN ONE POUR.
 - NO HORIZONTAL CONSTRUCTION JOINTS ARE ALLOWED IN COMBINED FOOTING.
 - 'T' REPRESENTS TOR STEEL GRADE HYSD/Fe-550 OF IS:1786. WITH CHARACTERISTIC YIELD STRENGTH OF Fe-550 N/ SQMM MINIMUM.
 - CLEAR COVER FOR MAIN REINFORCEMENT.
FOOTING:2 INCHES COLUMN:1.5 INCHES
BEAM:1 INCHES SLABS:1 INCHES

- ALL DIMENSIONS ARE IN FEET AND INCHES.
- ALL LEVELS ARE IN FEET.
- WHILE EXCAVATION IF ANY LOOSE POCKETS IS FOUND IN SOIL BRING NOTICE TO STRUCTURAL CONSULTANT.
- ONLY WRITTEN DIMENSION TO BE FOLLOWED. NEITHER THE DRAWINGS SHALL BE SCALED OUT NOR THE BARS SHALL BE COUNTED.
- ANY DISCREPANCY FOUND BETWEEN THIS DRAWING AND ARCHITECTURAL DRAWING SHALL BE BROUGHT TO THE NOTICE OF THE COMPETANT AUTHORITY.
- ALL REINFORCEMENT SHALL BE FREE FROM RUST, LOOSE SCALES & COAT OF PAINT.
- THIS DRAWING DO NOT BEAR ANY RISK OR RESPONSIBILITY FOR ANY FIELD LAPSES OR FAULTY WORKMANSHIP.

CLIENT:

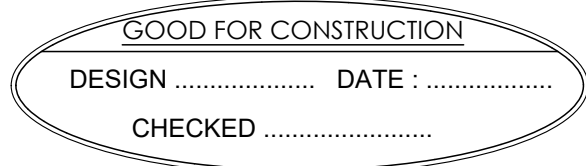SEAL / STAMP



PROJECT TITLE

CONSTRUCTION OF HOSPITAL BUILDING.

DRAWING TITLE

COLUMN LAYOUT

JOB NO

NSG00-2026

DWG NO

01















ORIENTATION:













STRUCTURAL DRAWING

ARCHITECTURAL & STRUCTURAL CONSULTANTS:



#01. MUNOLLI ARCADE, NEAR NAVANAGAR BRTS
BUS STOP PB ROAD, HUBLI.
PH. NO: 8097678405,8861607100

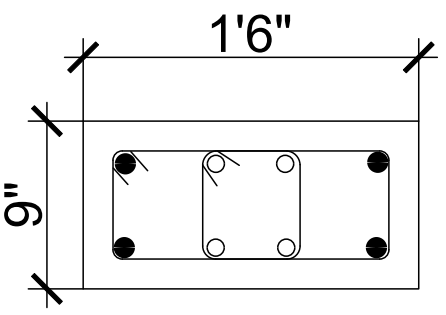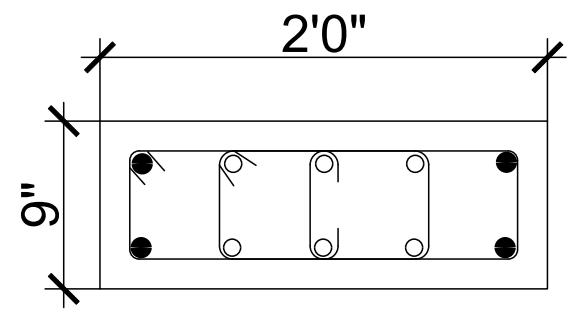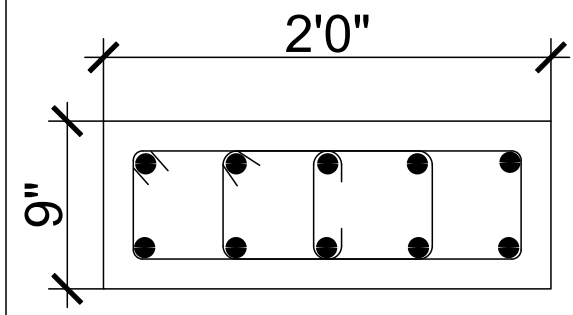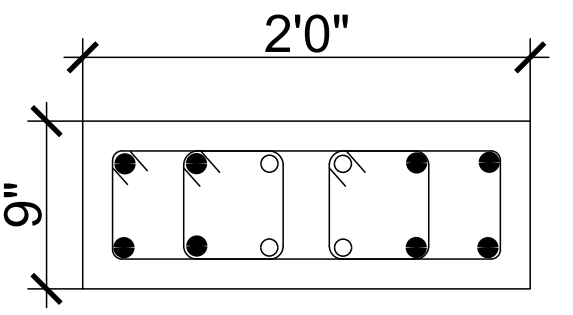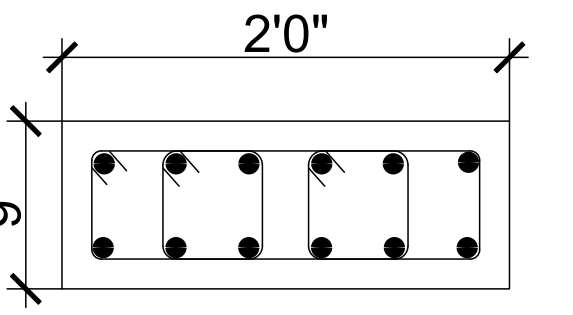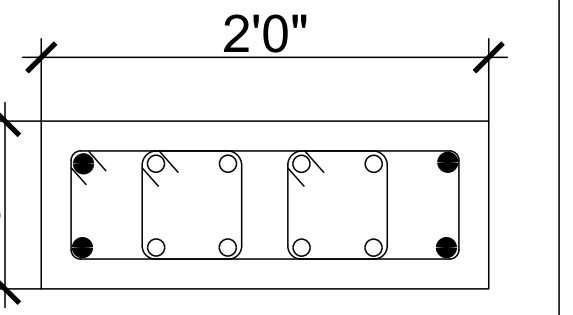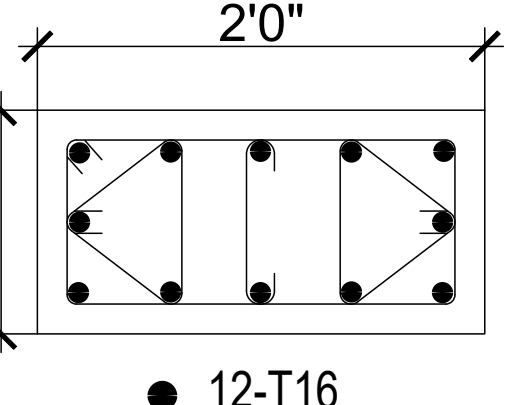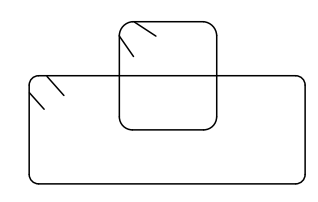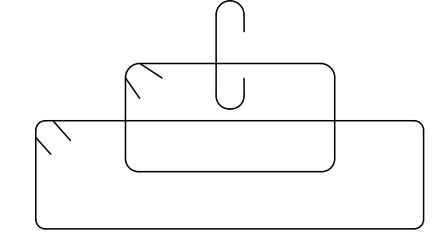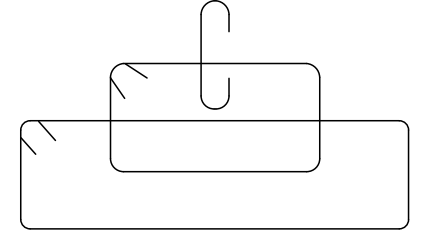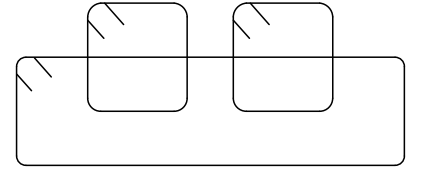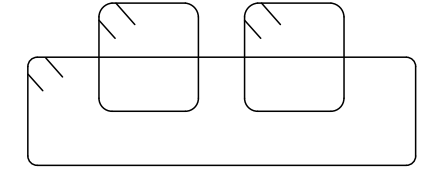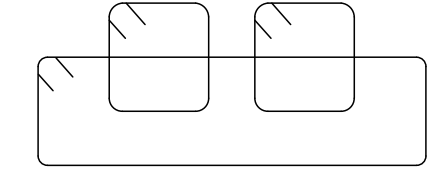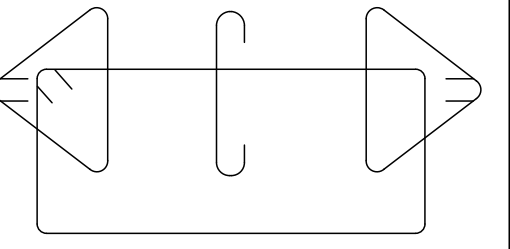COLUMN SCHEDULE							
COLUMN STEEL							
	M:25 Fe:550						
COLUMN SIZE	9"X1'6"	9"X2'0"	9"X2'0"	9"X2'0"	9"X2'0"	9"X2'0"	1'0"X2'0"
COLUMN LINKS T8@8"C/C							
COLUMN NO'S	C9,C17,C26&C33.	C8&C13.	C5,C16,C22&C25.	C4.	C6.	C7&C14.	C27&C30.
NUMBER OF COLUMNS	04	02	04	01	01	02	02

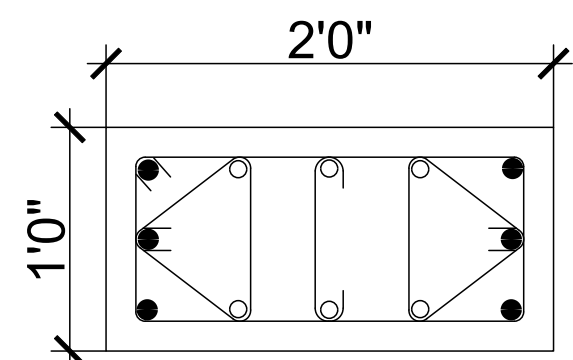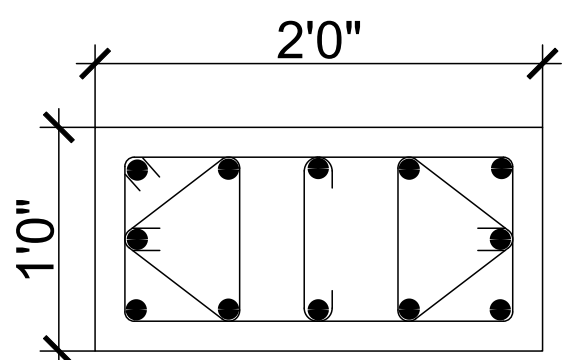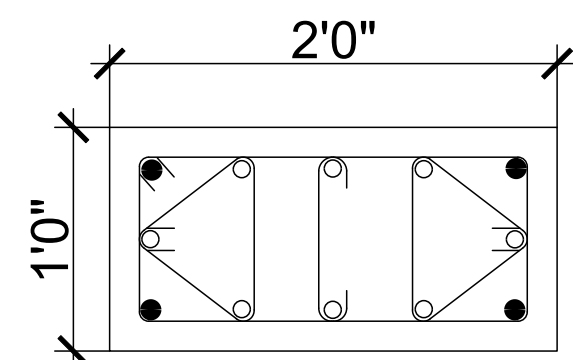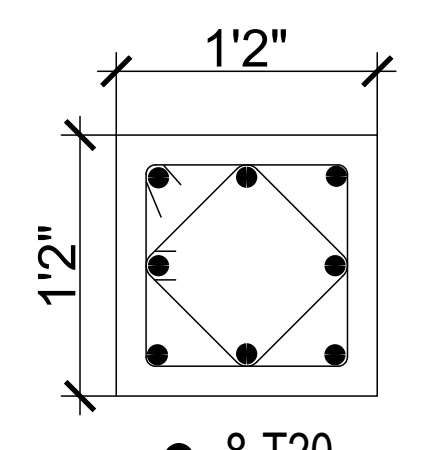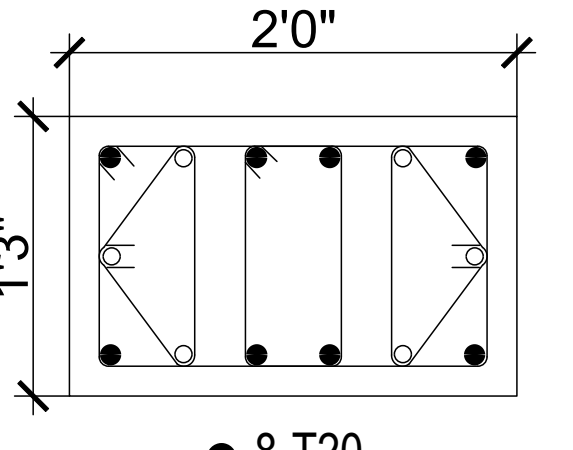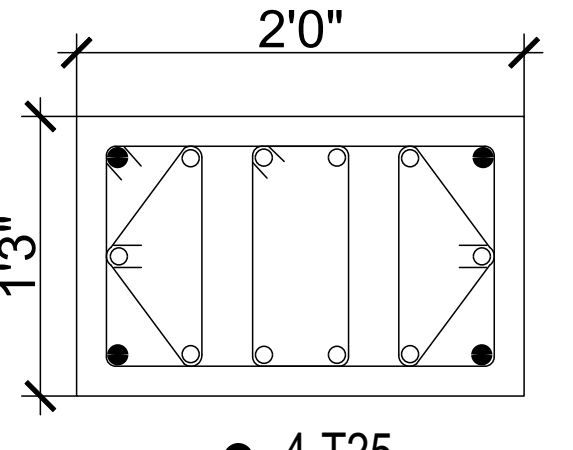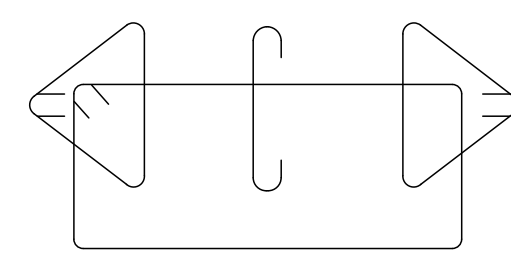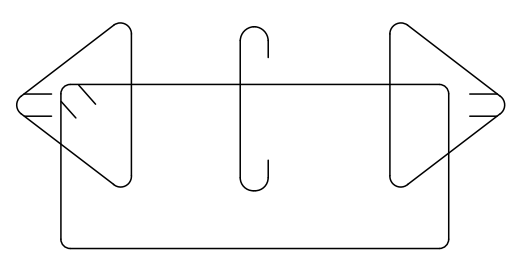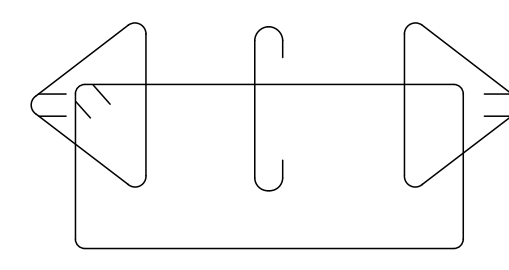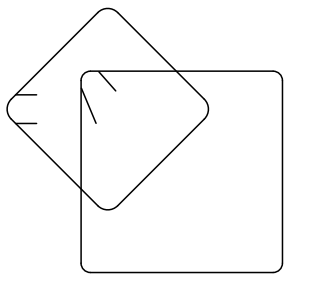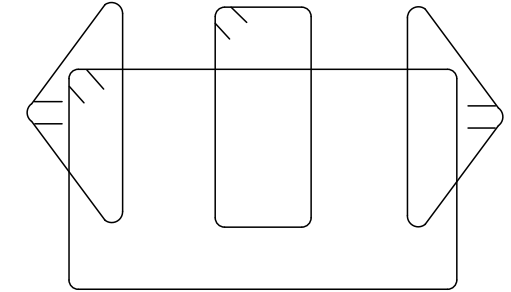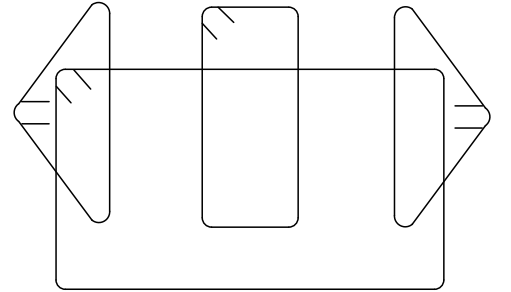COLUMN SCHEDULE							
COLUMN STEEL							
	M:25 Fe:550						
COLUMN SIZE	1'0"X2'0"	1'0"X2'0"	1'0"X2'0"	1'2"X1'2"	1'3"X2'0"	1'3"X2'0"	
COLUMN LINKS T8@8"C/C							
COLUMN NO'S	C2,C3,C15,C21, C28&C29.	C20&C32.	C1,C12&C31.	C23&C24.	C10&C18.	C11&C19.	
NUMBER OF COLUMNS	06	02	03	02	02	02	TOTAL=33

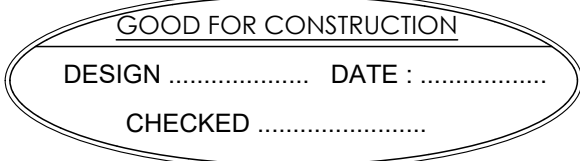
GENERAL NOTES:-

- THIS DRAWING TO BE READ IN CONJUNCTION WITH THE RELEVANT ARCHITECTURAL AND SERVICES DRAWINGS.
- BUILDING DESIGNED FOR B1+B2+G+3 FLOORS.
- GRADE OF CONCRETE FOR ALL RCC MEMBERS IN THE BUILDING IS M25.
- AT THE LOCATION WHERE FOOTING IS RESTING SBC IS 20.00T/SQ-M @5'0" MIN. FROM NGL. SBC SHALL BE RACTIFIED BEFORE LAYING THE PCC FROM CONSULTING PROFESSIONAL.
- FOR SETTING OUT OF THE BUILDING REFER ARCHITECTURAL DRAWING.
- COMBINED FOOTING CONCRETING TO BE DONE CONTINUOUSLY IN ONE POUR.
- NO HORIZONTAL CONSTRUCTION JOINTS ARE ALLOWED IN COMBINED FOOTING.
- 'T' REPRESENTS TOR STEEL GRADE HYSD/Fe-550 OF IS:1786. WITH CHARACTERISTIC YIELD STRENGTH OF Fe-550 N/ SQMM MINIMUM.
- CLEAR COVER FOR MAIN REINFORCEMENT.
FOOTING:2 INCHES COLUMN:1.5 INCHES
BEAM:1 INCHES SLABS:1 INCHES

- ALL DIMENSIONS ARE IN FEET AND INCHES.
- ALL LEVELS ARE IN FEET.
- WHILE EXCAVATION IF ANY LOOSE POCKETS IS FOUND IN SOIL BRING NOTICE TO STRUCTURAL CONSULTANT.
- ONLY WRITTEN DIMENSION TO BE FOLLOWED. NEITHER THE DRAWINGS SHALL BE SCALED OUT NOR THE BARS SHALL BE COUNTED.
- ANY DISCREPANCY FOUND BETWEEN THIS DRAWING AND ARCHITECTURAL DRAWING SHALL BE BROUGHT TO THE NOTICE OF THE COMPETANT AUTHORITY.
- ALL REINFORCEMENT SHALL BE FREE FROM RUST, LOOSE SCALES & COAT OF PAINT.
- THIS DRAWING DO NOT BEAR ANY RISK OR RESPONSIBILITY FOR ANY FIELD LAPSES OR FAULTY WORKMANSHIP.

CLIENT:

SEAL / STAMP



PROJECT TITLE

CONSTRUCTION OF HOSPITAL BUILDING.

DRAWING TITLE

COLUMN SCHEDULE

JOB NO
NSG00-2026

DWG NO
02


ORIENTATION:

STRUCTURAL DRAWING

ARCHITECTURAL & STRUCTURAL CONSULTANTS:



#01. MUNOLLI ARCADE, NEAR NAVANAGAR BRTS
BUS STOP PB ROAD, HUBLI.
PH. NO: 8097678405,8861607100

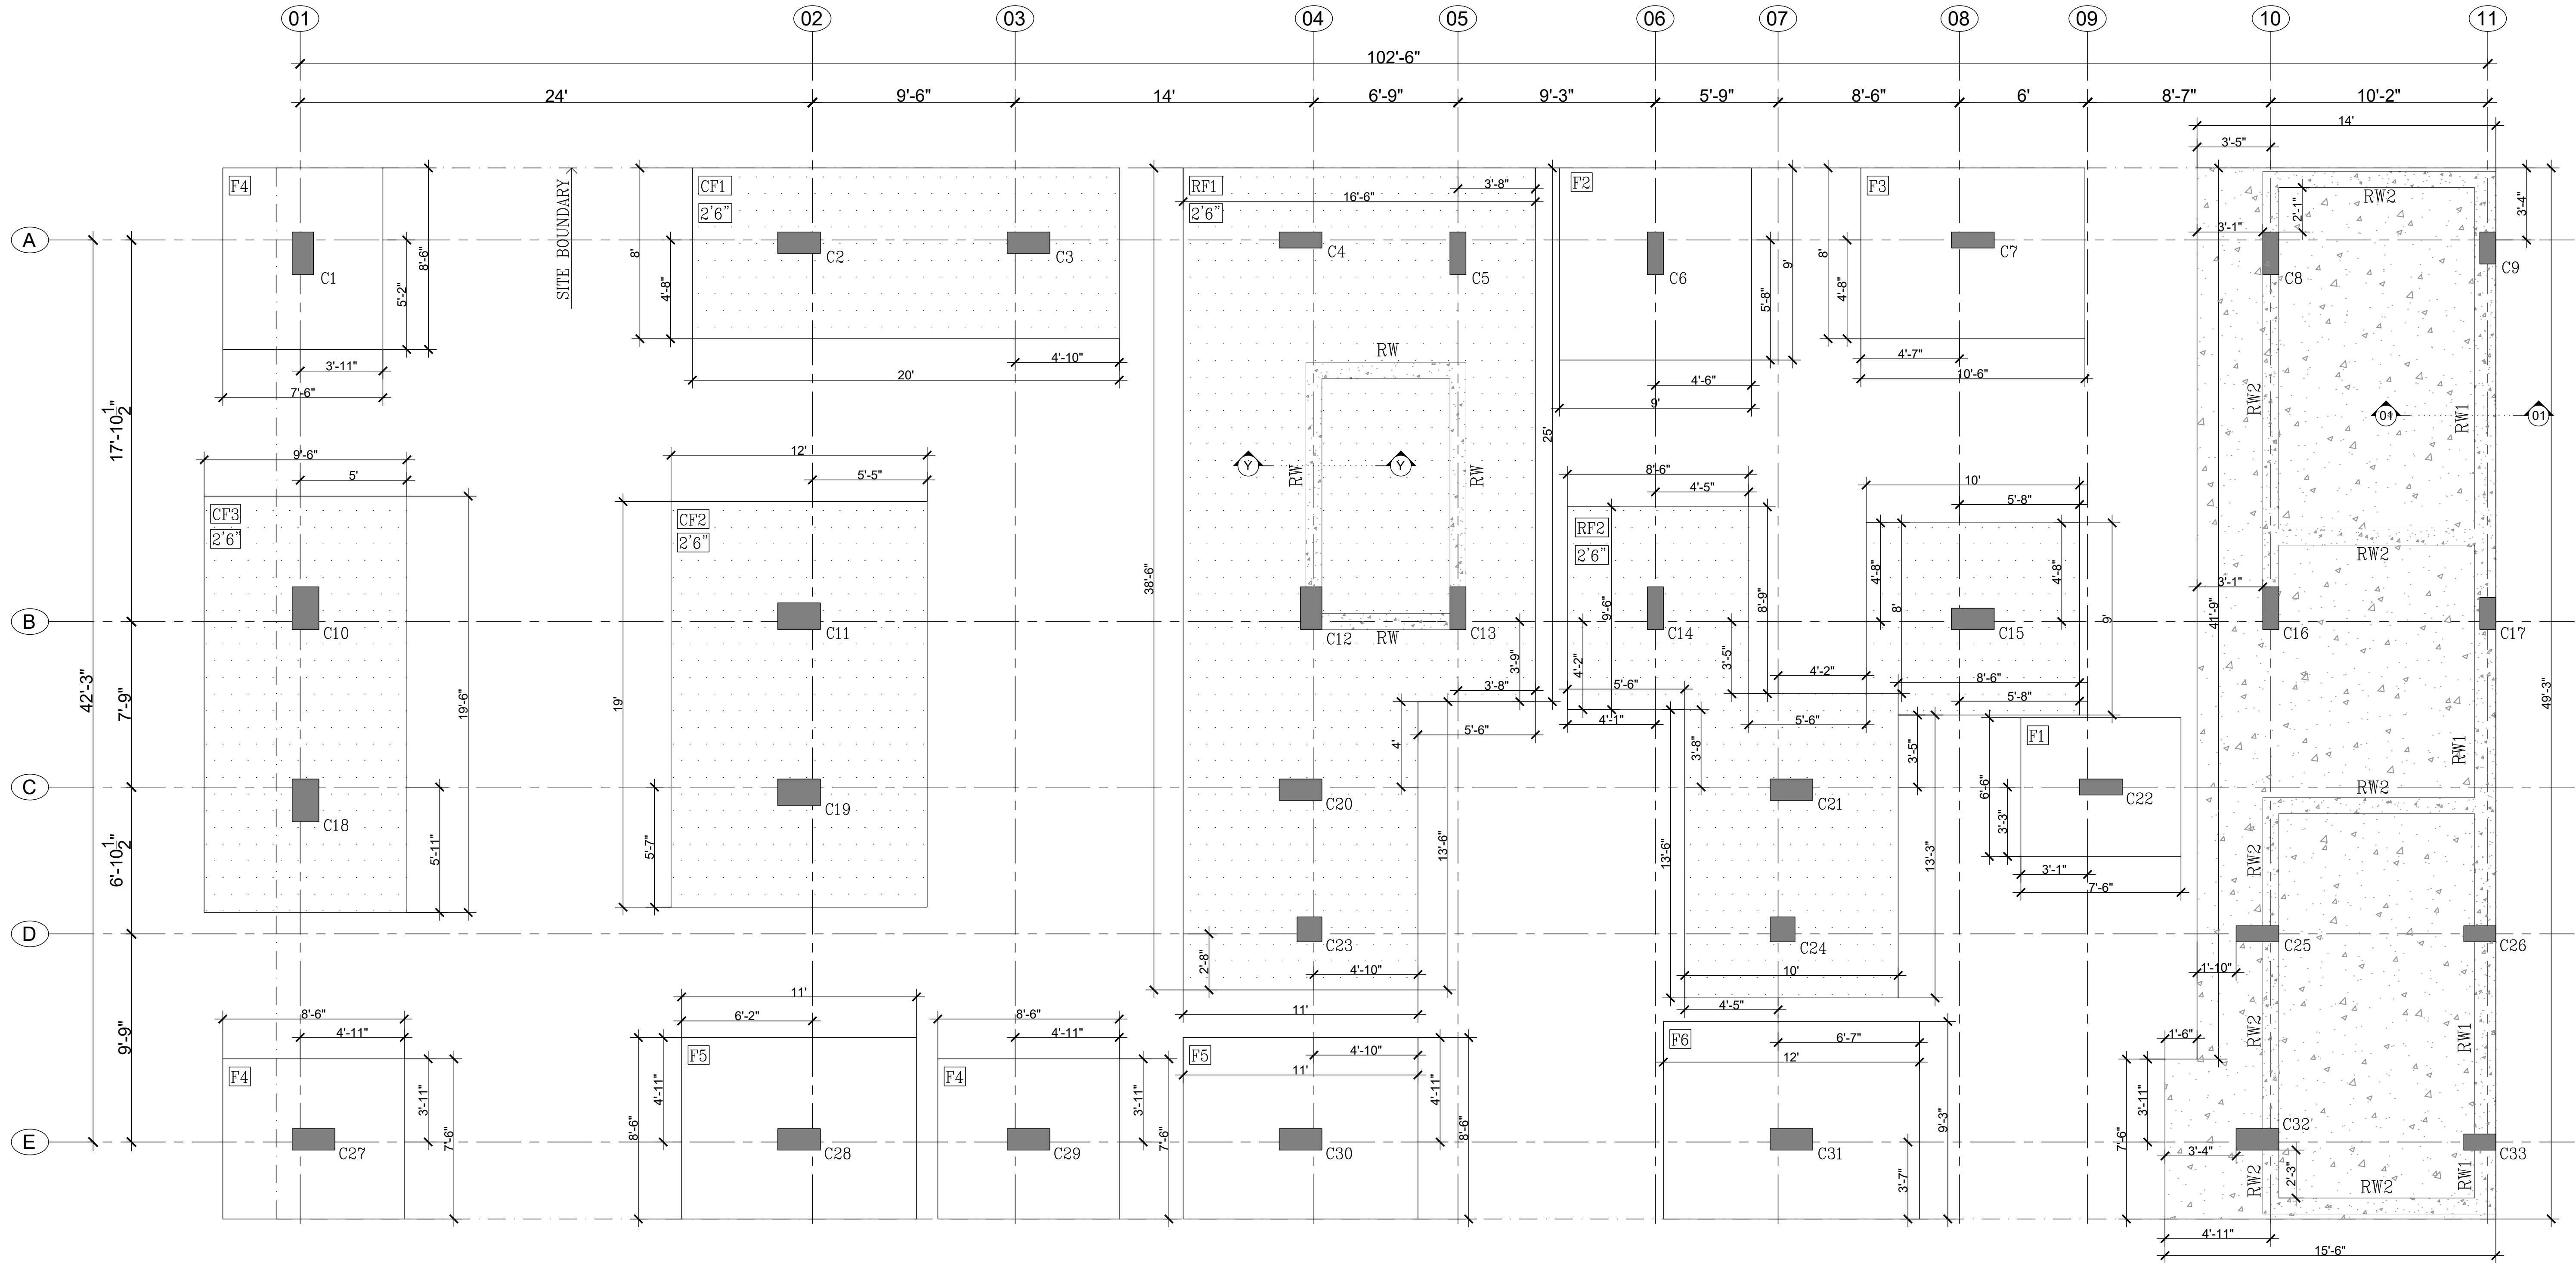


FOOTING LAYOUT

GENERAL NOTES:-

- THIS DRAWING TO BE READ IN CONJUNCTION WITH THE RELEVANT ARCHITECTURAL AND SERVICES DRAWINGS.
- BUILDING DESIGNED FOR B1+B2+G+3 FLOORS.
- GRADE OF CONCRETE FOR ALL RCC MEMBERS IN THE BUILDING IS M25.
- AT THE LOCATION WHERE FOOTING IS RESTING SBC IS 20.00T/SQ-M @50" MIN. FROM NGL. SBC SHALL BE RACTIFIED BEFORE LAYING THE PCC FROM CONSULTING PROFESSIONAL.
- FOR SETTING OUT OF THE BUILDING REFER ARCHITECTURAL DRAWING.
- COMBINED FOOTING CONCRETING TO BE DONE CONTINUOUSLY IN ONE POUR.
- NO HORIZONTAL CONSTRUCTION JOINTS ARE ALLOWED IN COMBINED FOOTING.
- "T" REPRESENTS TOR STEEL GRADE HYSD/Fe-550 OF IS:1786. WITH CHARACTERISTIC YIELD STRENGTH OF Fe-550 N/ SQMM MINIMUM.
- CLEAR COVER FOR MAIN REINFORCEMENT.
FOOTING:2 INCHES COLUMN:1.5 INCHES
BEAM:1 INCHES SLABS:1 INCHES
- ALL DIMENSIONS ARE IN FEET AND INCHES.
- ALL LEVELS ARE IN FEET.
- WHILE EXCAVATION IF ANY LOOSE POCKETS IS FOUND IN SOIL BRING NOTICE TO STRUCTURAL CONSULTANT.
- ONLY WRITTEN DIMENSION TO BE FOLLOWED. NEITHER THE DRAWINGS SHALL BE SCALED OUT NOR THE BARS SHALL BE COUNTED.
- ANY DISCREPANCY FOUND BETWEEN THIS DRAWING AND ARCHITECTURAL DRAWING SHALL BE BROUGHT TO THE NOTICE OF THE COMPETANT AUTHORITY.
- ALL REINFORCEMENT SHALL BE FREE FROM RUST, LOOSE SCALES & COAT OF PAINT.
- THIS DRAWING DO NOT BEAR ANY RISK OR RESPONSIBILITY FOR ANY FIELD LAPSES OR FAULTY WORKMANSHIP.

CLIENT:

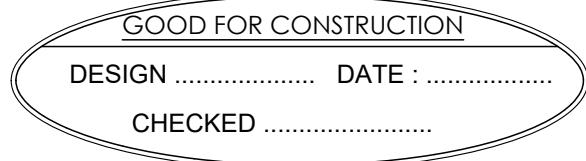SEAL / STAMP



PROJECT TITLE

CONSTRUCTION OF HOSPITAL BUILDING.

DRAWING TITLE

FOOTING LAYOUT

JOB NO

NSG00-2026

DWG NO

03

ORIENTATION:

STRUCTURAL DRAWING


ARCHITECTURAL & STRUCTURAL CONSULTANTS:




#01. MUNOLLI ARCADE, NEAR NAVANAGAR BRTS
BUS STOP PB ROAD, HUBLI.
PH. NO: 8097678405,8861607100

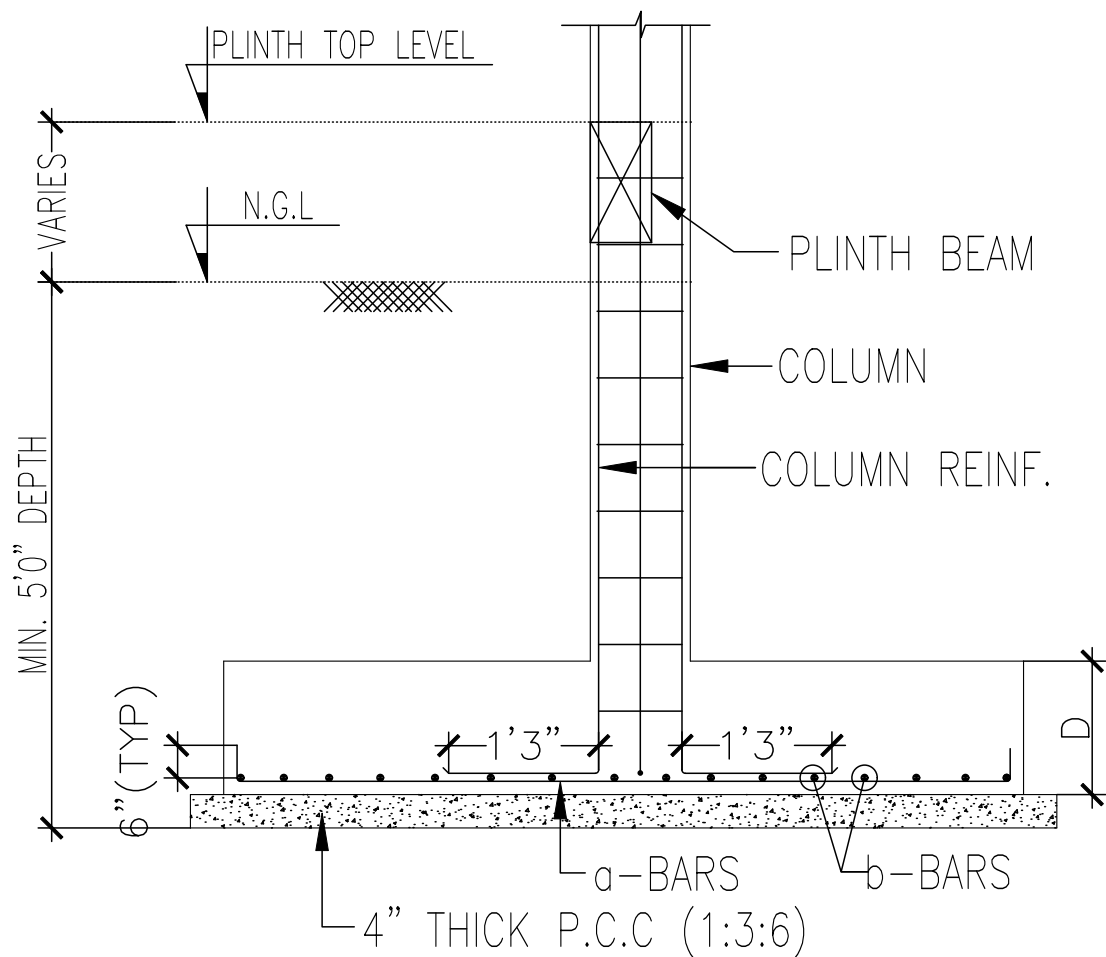SCHEDULE OF R.C.C FOOTINGS


FOOTING NO.	COLUMN SIZE		FOOTING SIZE		FOOTING DEPTH	FOOTING REINFORCEMENT	
	X	Y	B	L		AT BOTTOM ('a' & 'b' BARS)	AT TOP ('a' & 'b' BARS)
F1	9"	2'0"	6'6"	7'6"	2'0'	T10@5"C/C	---
F2	9"	2'0"	9'0"	9'0'	2'6"	T12@5"C/C	---
F3	9"	2'0"	8'0"	10'6"	2'6"	T12@5"C/C	---
F4	1'0"	2'0"	7'6"	8'6"	2'3"	T12@6"C/C	---
F5	1'0"	2'0"	8'6"	11'0"	2'6"	T12@5"C/C	---
F6	1'0"	2'0"	9'3"	12'0"	2'6"	T16@6"C/C	---
CF1	REFER PLAN		REFER PLAN		2'6"	T12@5"C/C	T10@8"C/C
CF2	REFER PLAN		REFER PLAN		2'6"	T16@6"C/C	T10@8"C/C
CF3	REFER PLAN		REFER PLAN		2'6"	T12@5"C/C	T10@8"C/C
RF1	REFER PLAN		REFER PLAN		2'6"	T16@6"C/C	T10@8"C/C
RF2	REFER PLAN		REFER PLAN		2'6"	T12@5"C/C	T10@8"C/C




SECTION X-X

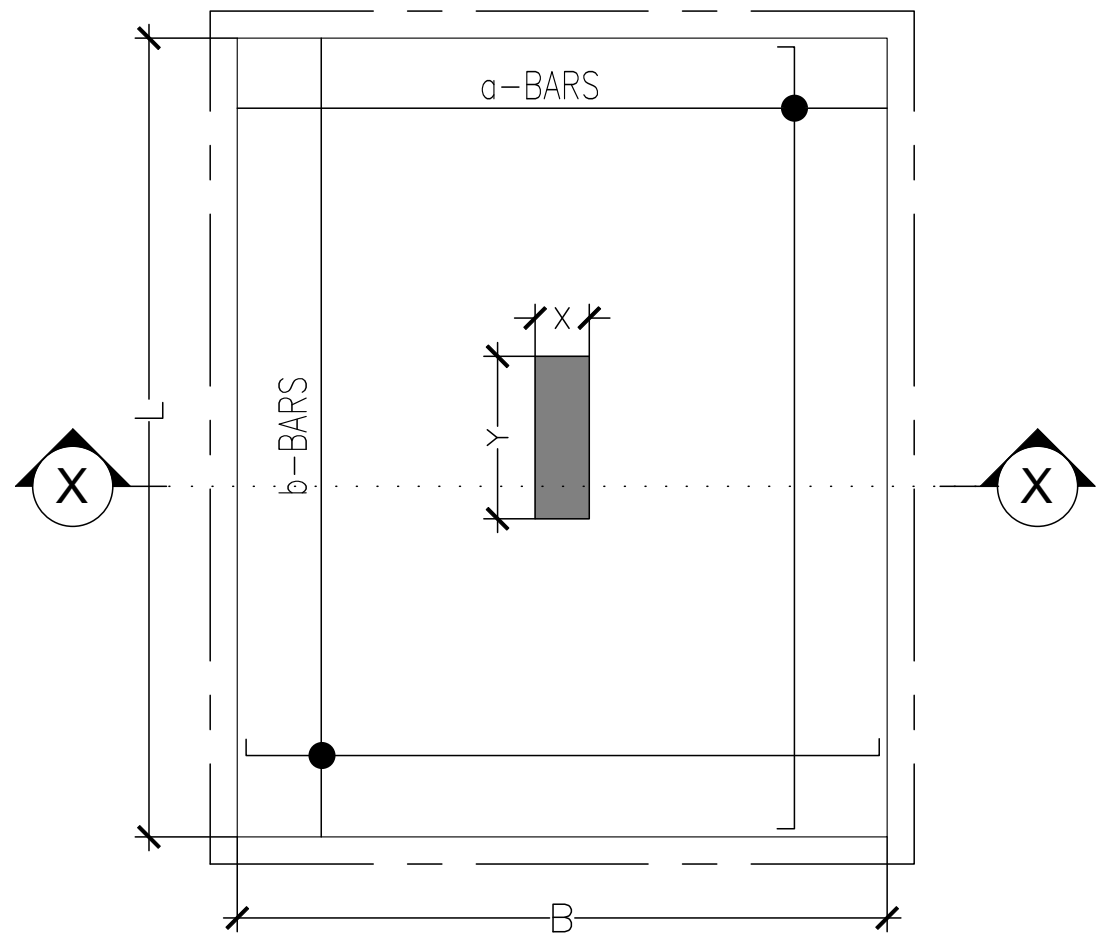

TYPICAL ISOLATED R.C. FOOTING

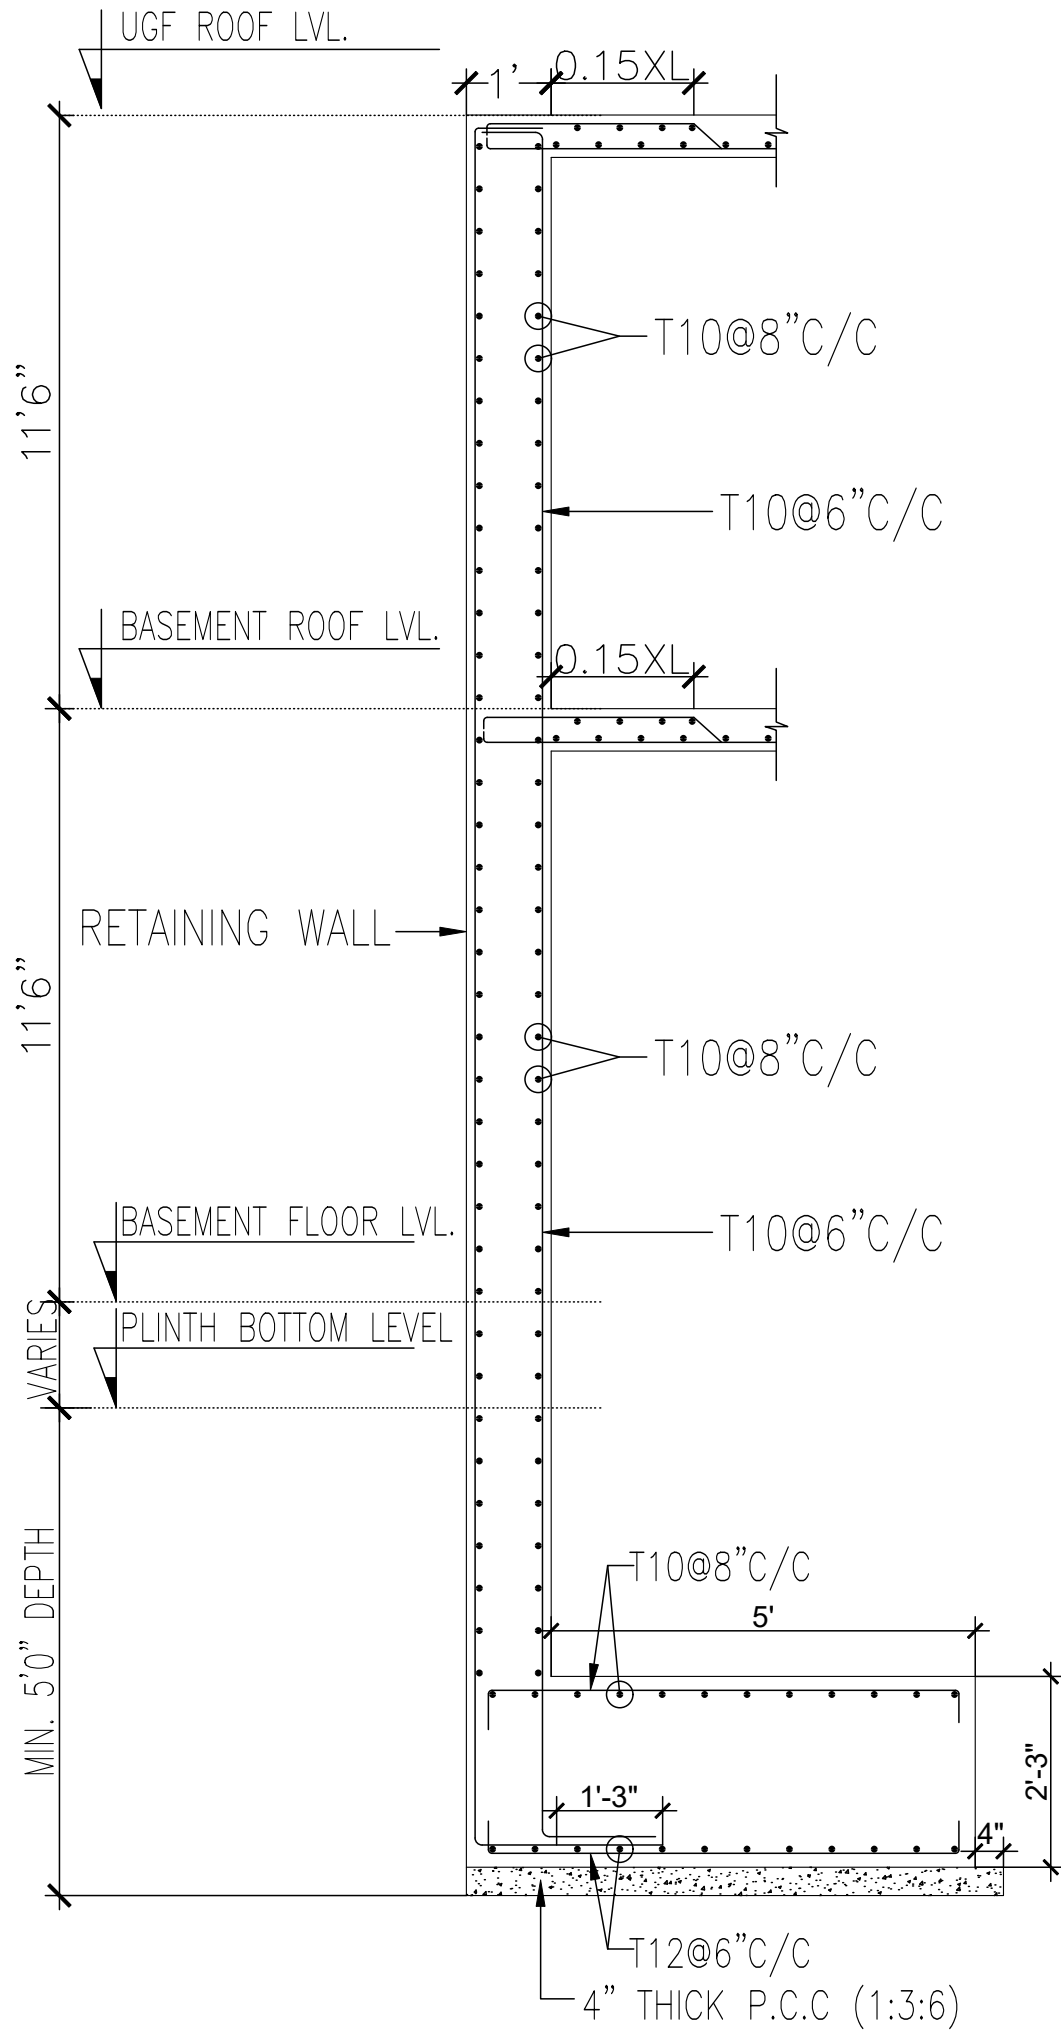

SECTION 01-01
RETAINING WALL-RW1

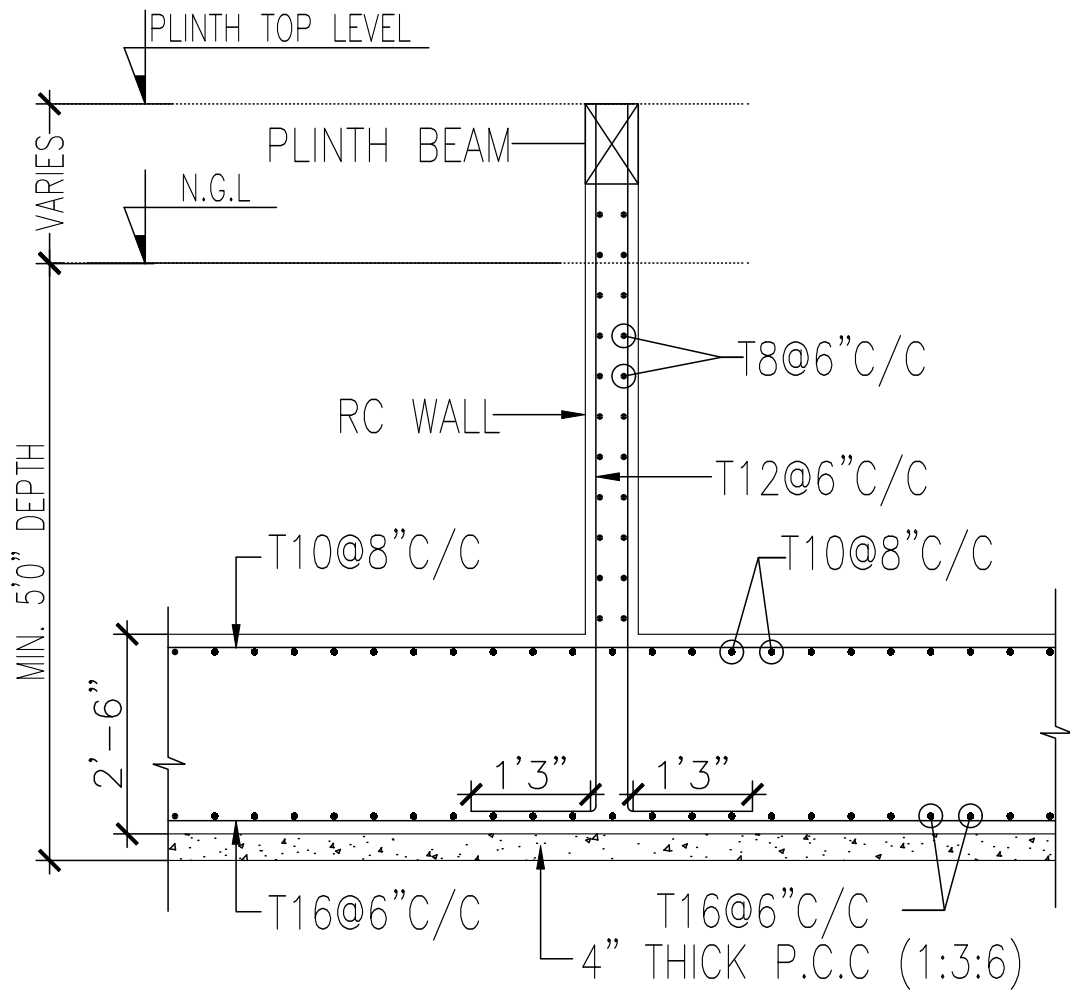

SECTION Y-Y
RC WALL DETAILS

NOTE:
1.RC WALL TO BE PROVIDED
UP TO PLINTH BOTTOM
LEVEL FOR LIFT PORTION.

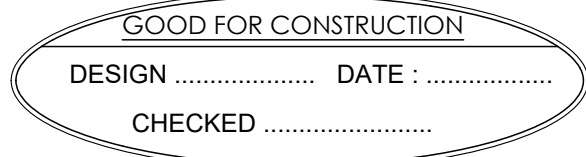
GENERAL NOTES:-

- THIS DRAWING TO BE READ IN CONJUNCTION WITH THE RELEVANT ARCHITECTURAL AND SERVICES DRAWINGS.
- BUILDING DESIGNED FOR B1+B2+G+3 FLOORS.
- GRADE OF CONCRETE FOR ALL RCC MEMBERS IN THE BUILDING IS M25.
- AT THE LOCATION WHERE FOOTING IS RESTING SBC IS 20.00T/SQ-M @5'0" MIN. FROM NGL. SBC SHALL BE RACTIFIED BEFORE LAYING THE PCC FROM CONSULTING PROFESSIONAL.
- FOR SETTING OUT OF THE BUILDING REFER ARCHITECTURAL DRAWING.
- COMBINED FOOTING CONCRETING TO BE DONE CONTINUOUSLY IN ONE POUR.
- NO HORIZONTAL CONSTRUCTION JOINTS ARE ALLOWED IN COMBINED FOOTING.
- 'T' REPRESENTS TOR STEEL GRADE HYSD/Fe-550 OF IS:1786. WITH CHARACTERISTIC YIELD STRENGTH OF Fe-550 N/ SQMM MINIMUM.
- CLEAR COVER FOR MAIN REINFORCEMENT.
FOOTING:2 INCHES COLUMN:1.5 INCHES
BEAM:1 INCHES SLABS:1 INCHES

- ALL DIMENSIONS ARE IN FEET AND INCHES.
- ALL LEVELS ARE IN FEET.
- WHILE EXCAVATION IF ANY LOOSE POCKETS IS FOUND IN SOIL BRING NOTICE TO STRUCTURAL CONSULTANT.
- ONLY WRITTEN DIMENSION TO BE FOLLOWED. NEITHER THE DRAWINGS SHALL BE SCALED OUT NOR THE BARS SHALL BE COUNTED.
- ANY DISCREPANCY FOUND BETWEEN THIS DRAWING AND ARCHITECTURAL DRAWING SHALL BE BROUGHT TO THE NOTICE OF THE COMPETANT AUTHORITY.
- ALL REINFORCEMENT SHALL BE FREE FROM RUST, LOOSE SCALES & COAT OF PAINT.
- THIS DRAWING DO NOT BEAR ANY RISK OR RESPONSIBILITY FOR ANY FIELD LAPSES OR FAULTY WORKMANSHIP.

CLIENT:

SEAL / STAMP



PROJECT TITLE

CONSTRUCTION OF HOSPITAL BUILDING.

DRAWING TITLE

FOOTING SCHEDULE AND DETAILS

JOB NO
NSG00-2026

DWG NO
04

ORIENTATION:
N

STRUCTURAL DRAWING

ARCHITECTURAL & STRUCTURAL CONSULTANTS:



#01. MUNOLLI ARCADE, NEAR NAVANAGAR BRTS
BUS STOP PB ROAD, HUBLI.
PH. NO: 8097678405,8861607100